
TƯ VẤN SƠ BỘ THOÁT NẠN (lần 3, 30/10/2026) – tham khảo, không phải kết luận thẩm định. Chi tiết: tu_van_thiet_ke_v3.md
TẦNG 1: lối ra của buồng thang (3.4.7)

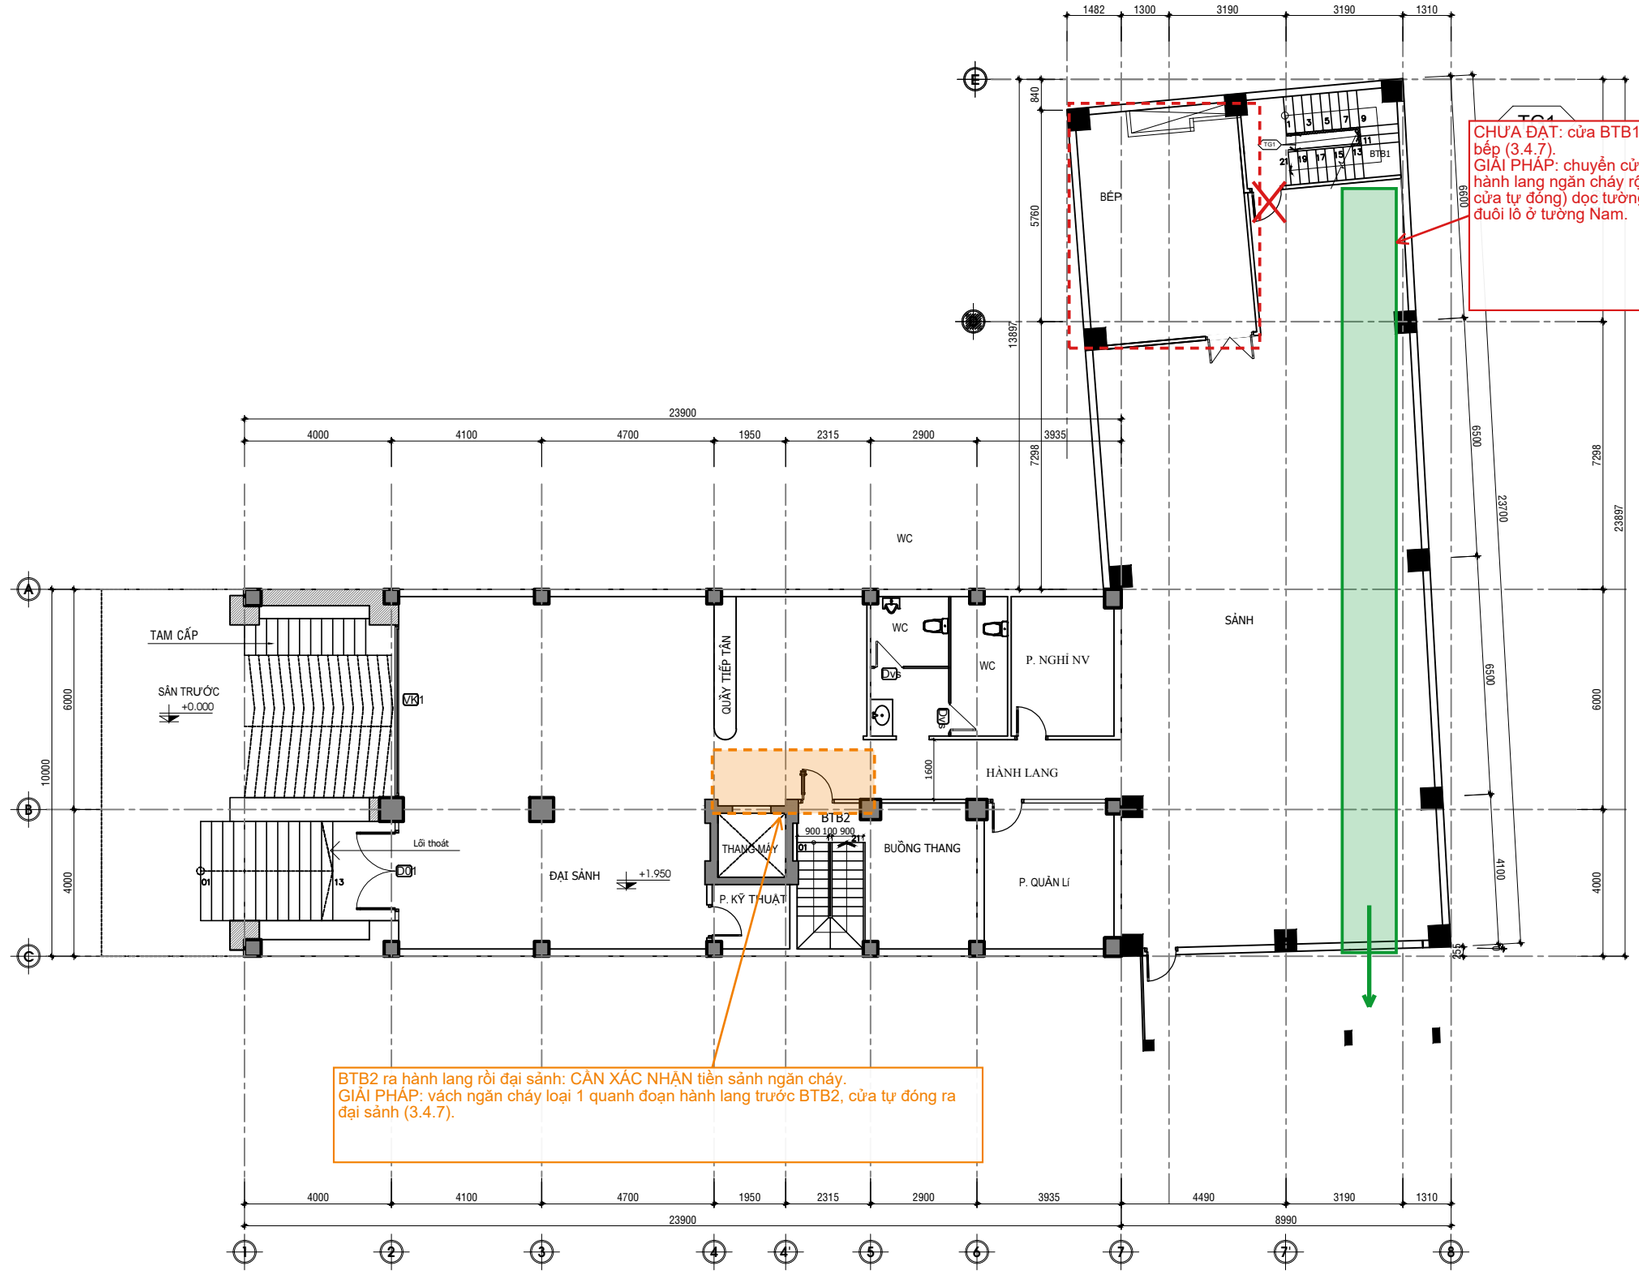

MẶT BẰNG TẦNG 1_TL:1/100

CTY TNHH TƯ VẤN ĐẦU TƯ CIC

ĐC: VÕ VĂN TẦN - P.TÂN BÌNH
TP ĐỒNG XOÀI - TỈNH BÌNH PHƯỚC
Email: cic.binhphuoc@gmail.com
Tel:0988.600.677
fax: 06513.888.824

GIÁM ĐỐC
Ks. LÊ ĐỨC PHÚC

CHỦ TRÌ
Kts. ĐẶNG CÔNG THÀNH

QUẢN LÝ KỸ THUẬT
Kts. ĐẶNG CÔNG THÀNH

THỂ HIỆN
Kts. ĐẶNG CÔNG THÀNH

CHỦ ĐẦU TƯ
TRẦN VĂN HÙNG


CÔNG TRÌNH
KHÁCH SẠN HOÀNG HÙNG

HẠNG MỤC
KHÁCH SẠN

TÊN BẢN VẼ
MẶT BẰNG TẦNG 1

TỈ LỆ BV:	1:100	BẢN VẼ TKTC
NGÀY HT:	06/2025	KT:04 /27

TƯ VẤN SƠ BỘ THOÁT NẠN (lần 3, 30/10/2026) – tham khảo, không phải kết luận thẩm định. Chi tiết: tu_van_thiet_ke_v3.md
TẦNG 2: hội trường đãi tiệc ~280 người (Bảng G.9, 1,5 m²/người)

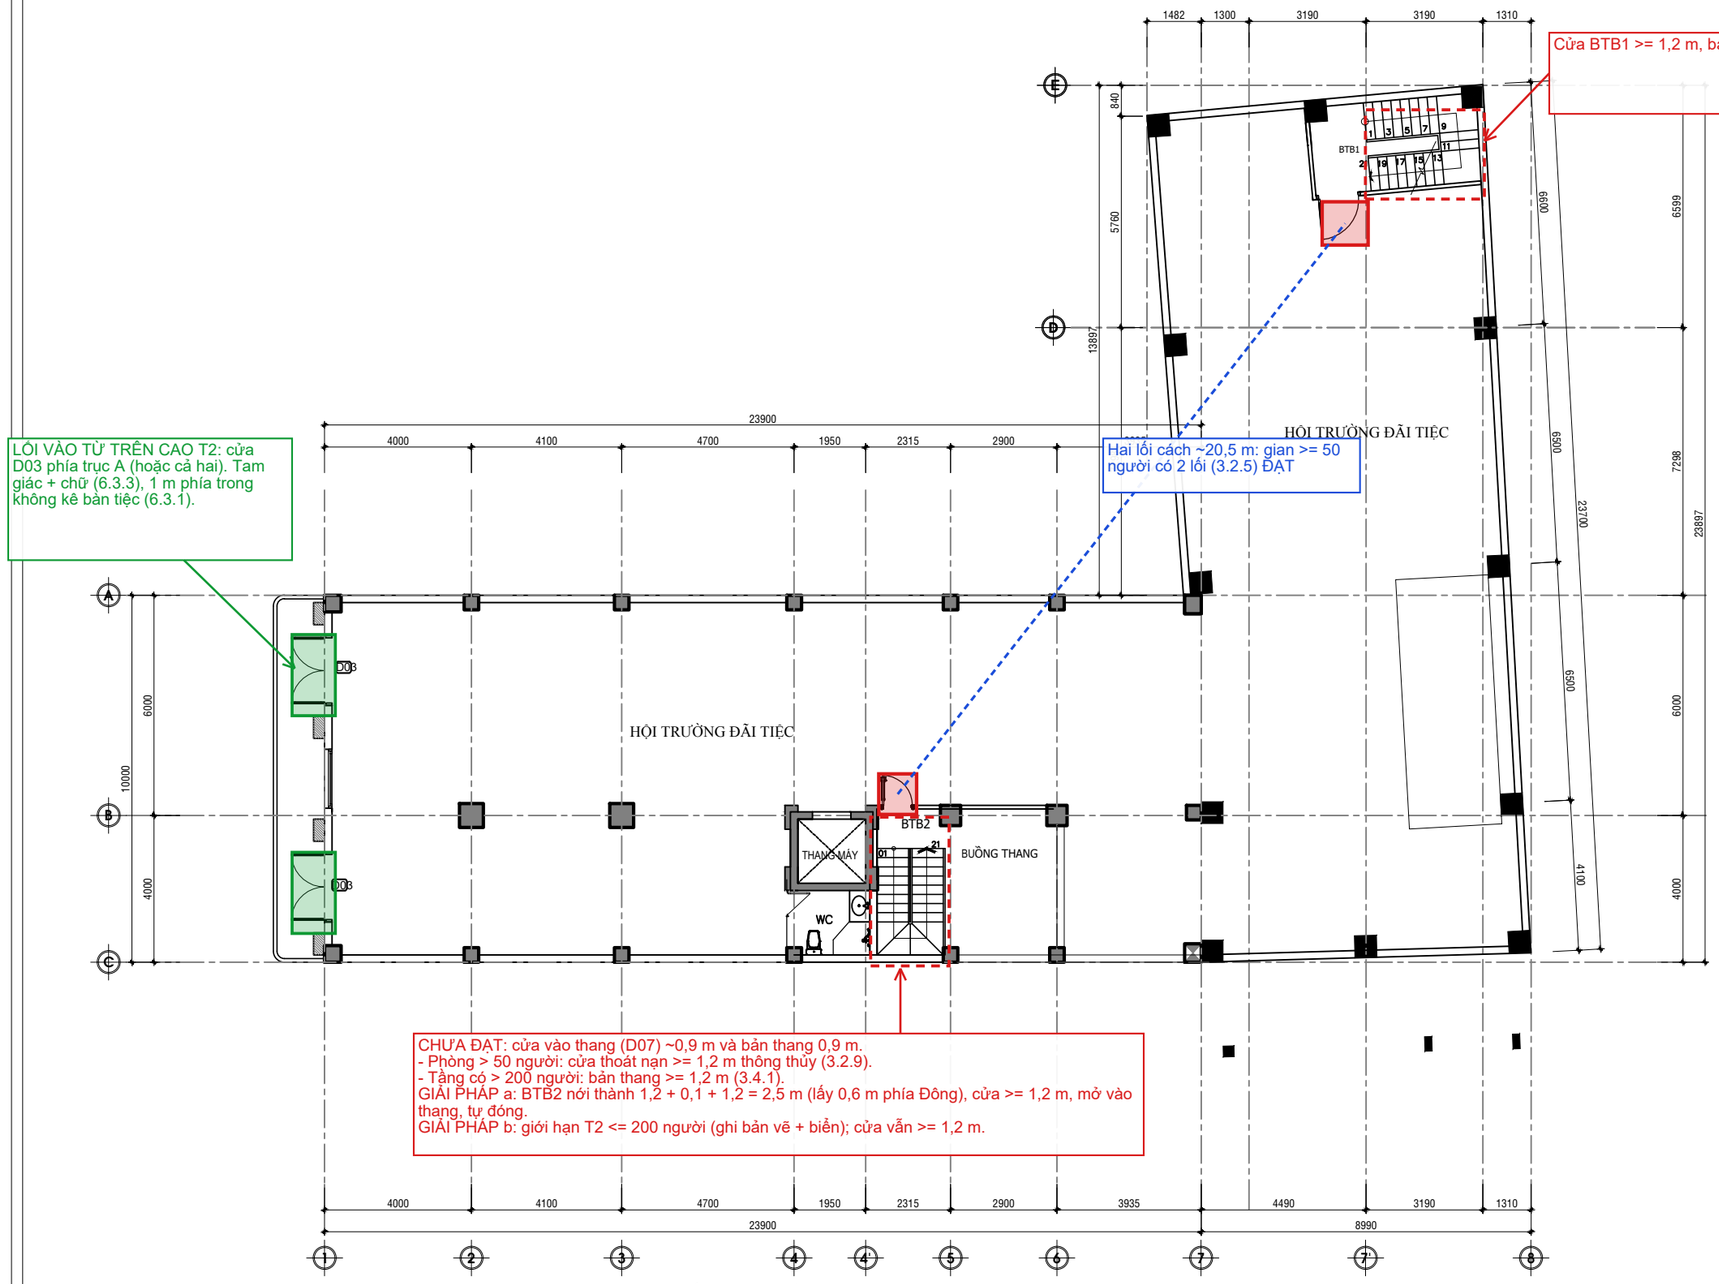

MẶT BẰNG TẦNG 2_TL:1/100

CTY TNHH TƯ VẤN ĐẦU TƯ
CIC
ĐC: VÕ VĂN TẦN - P.TÂN BÌNH
TP ĐỒNG XOÀI - TỈNH BÌNH PHƯỚC
Email: cic.binhphuoc@gmail.com
Tel:0988.600.677
fax: 06513.888.824

GIÁM ĐỐC
Ks. LÊ ĐỨC PHÚC

CHỦ TRÌ
Kts. ĐẶNG CÔNG THÀNH

QUẢN LÝ KỸ THUẬT
Kts. ĐẶNG CÔNG THÀNH

THỂ HIỆN
Kts. ĐẶNG CÔNG THÀNH

CHỦ ĐẦU TƯ
TRẦN VĂN HÙNG

CÔNG TRÌNH
KHÁCH SẠN HOÀNG HÙNG

HẠNG MỤC
KHÁCH SẠN

TÊN BẢN VẼ
MẶT BẰNG TẦNG 2

TỈ LỆ BV:	1:100	BẢN VẼ TKTC
NGÀY HT:	06/2025	KT:05 /27

TƯ VẤN SƠ BỘ THOÁT NẠN (lần 3, 30/10/2026) – tham khảo, không phải kết luận thẩm định. Chi tiết: tu_van_thiet_ke_v3.md
TẦNG 3 (điển hình T3–T9): buồng thang không nhiễm khói (3.4.13)

PHÂN TÁN (3.2.8): D ≈ 40,6 m; L hai cửa thang ≈ 20,5 m >= D/2 = 20,3 m (sát). Có sprinkler toàn nhà: L >= D/3 = 13,6 m. Ghi rõ sprinkler trên bản vẽ.


KHOANG ĐỆM BTB1 (đề xuất) ~1,9 x 2,1 m ≈ 4 m²: quây đầu hành lang cánh Đông trước cửa D07, không mất phòng. Tăng áp như BTB2. Không làm N1: sát nhà dân.

LỐI VÀO TỪ TRÊN CAO: cửa ban công VIP 01 (mặt Tây, đối diện bãi đỗ) mỗi tầng T3–T9. Tam giác đỏ/vàng >= 150 mm, chữ >= 25 mm (6.3.3); 1 m phía trong trống (6.3.1).

Cửa sổ giữa mặt Tây là WC: không chọn làm lối vào trên cao.

KHOANG ĐỆM BTB2 (đề xuất) ~2,7 x 2,3 m ≈ 6 m² (>= 3 m², 3.4.9): dùng phần trống phía Đông về thang trong buồng thang; cửa từ hành lang vào khoang đệm rồi vào thang. Tăng áp khoang đệm + buồng thang, cấp khí độc lập, điện 2 nguồn (3.4.13, Phụ lục D).

Bản thang 0,9 m -> 1,2 m vì T2 > 200 người (3.4.1), suốt chiều cao nhà.

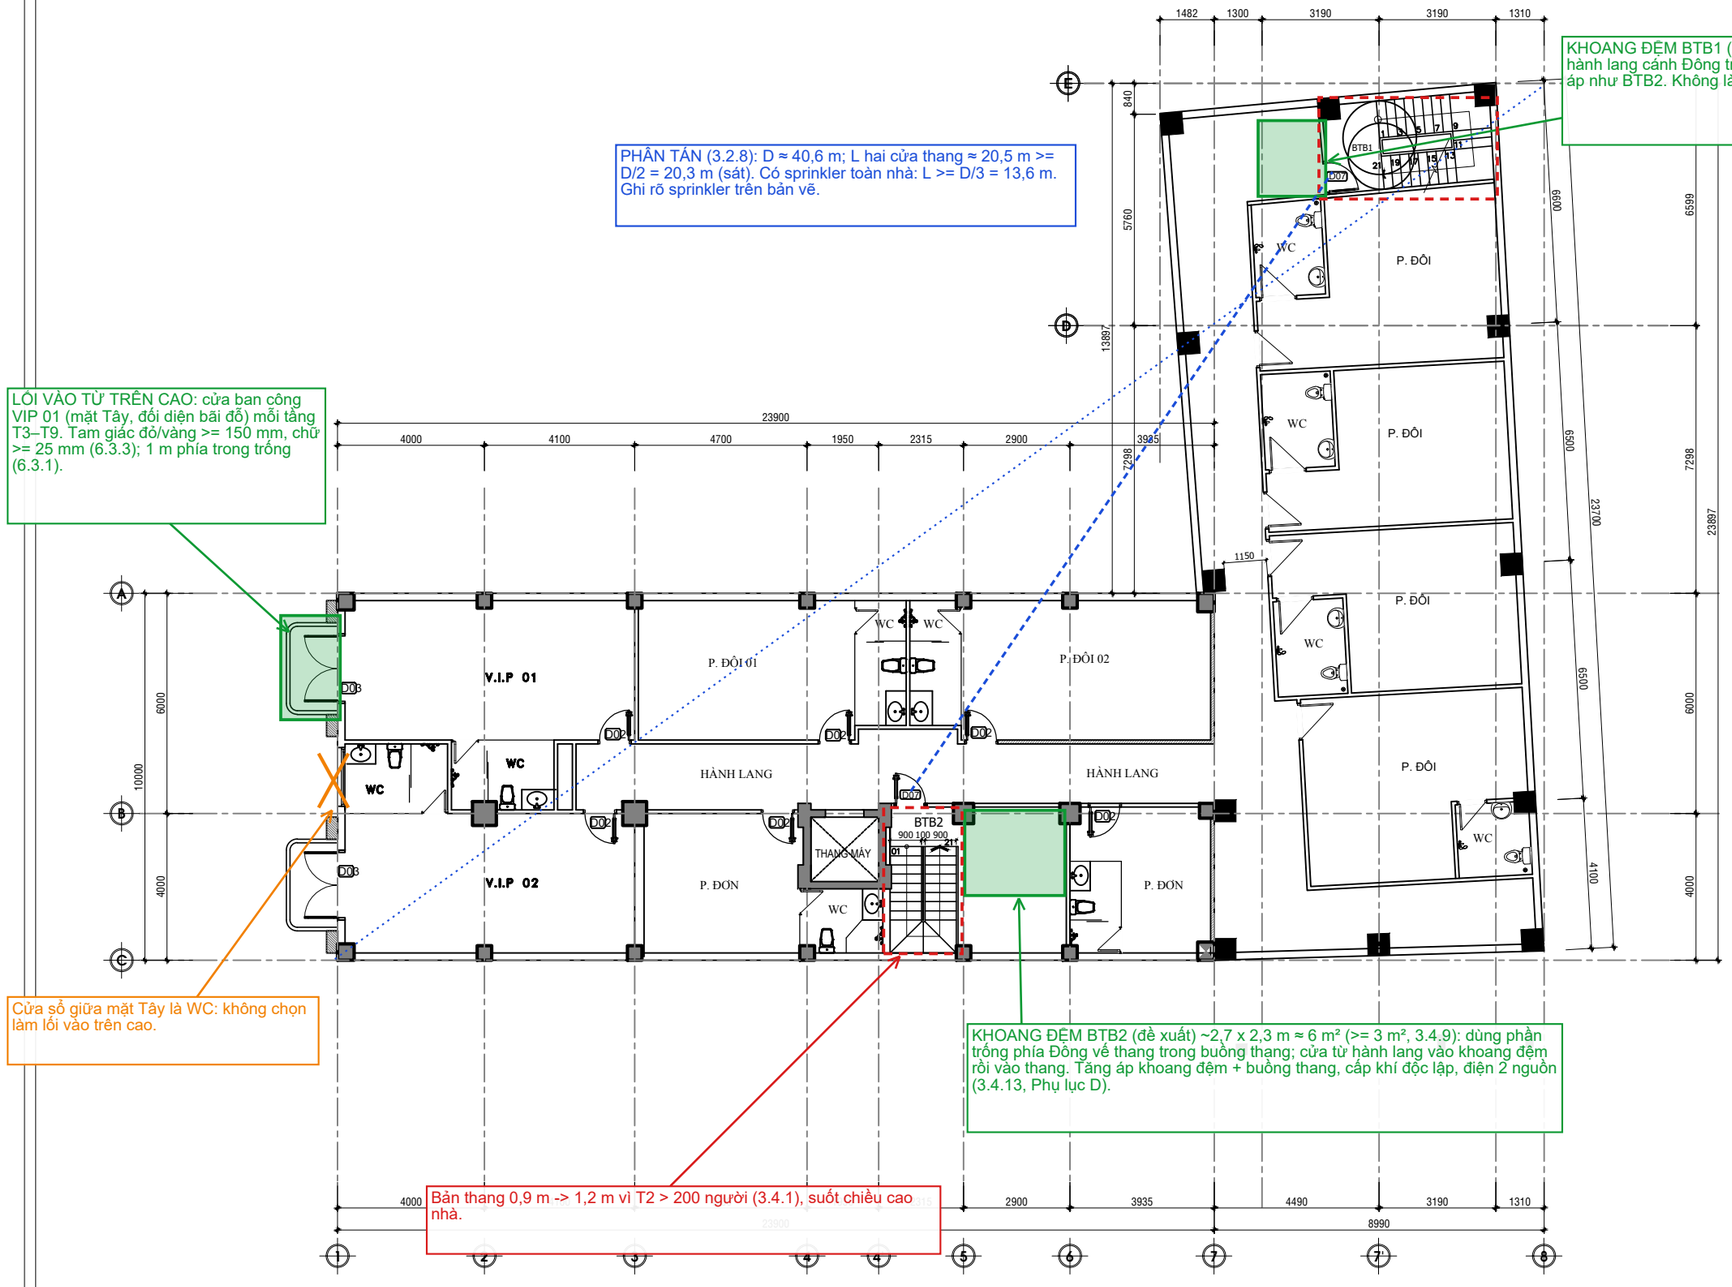

MẶT BẰNG TẦNG 3_TL:1/100

CTY TNHH TƯ VẤN ĐẦU TƯ CIC
ĐC: VÕ VĂN TÀN - P.TÂN BÌNH
TP ĐỒNG XOÀI - TỈNH BÌNH PHƯỚC
Email: cic.binhphuoc@gmail.com
Tel:0988.600.677
fax: 06513.888.824

GIÁM ĐỐC
Ks. LÊ ĐỨC PHÚC

CHỦ TRÌ
Kts. ĐẶNG CÔNG THÀNH

QUẢN LÝ KỸ THUẬT
Kts. ĐẶNG CÔNG THÀNH

THỂ HIỆN
Kts. ĐẶNG CÔNG THÀNH

CHỦ ĐẦU TƯ
TRẦN VĂN HÙNG


CÔNG TRÌNH
KHÁCH SẠN HOÀNG HÙNG

HẠNG MỤC
KHÁCH SẠN

TÊN BẢN VẼ
MẶT BẰNG TẦNG 3

TỈ LỆ BV:	1:100	BẢN VẼ TKTC
NGÀY HT:	06/2025	KT:06 /27

TƯ VẤN SƠ BỘ THOÁT NẠN (lần 3, 30/10/2026) – tham khảo, không phải kết luận thẩm định. Chi tiết: tu_van_thiet_ke_v3.md
TẦNG 10 (sân thượng): số lối ra

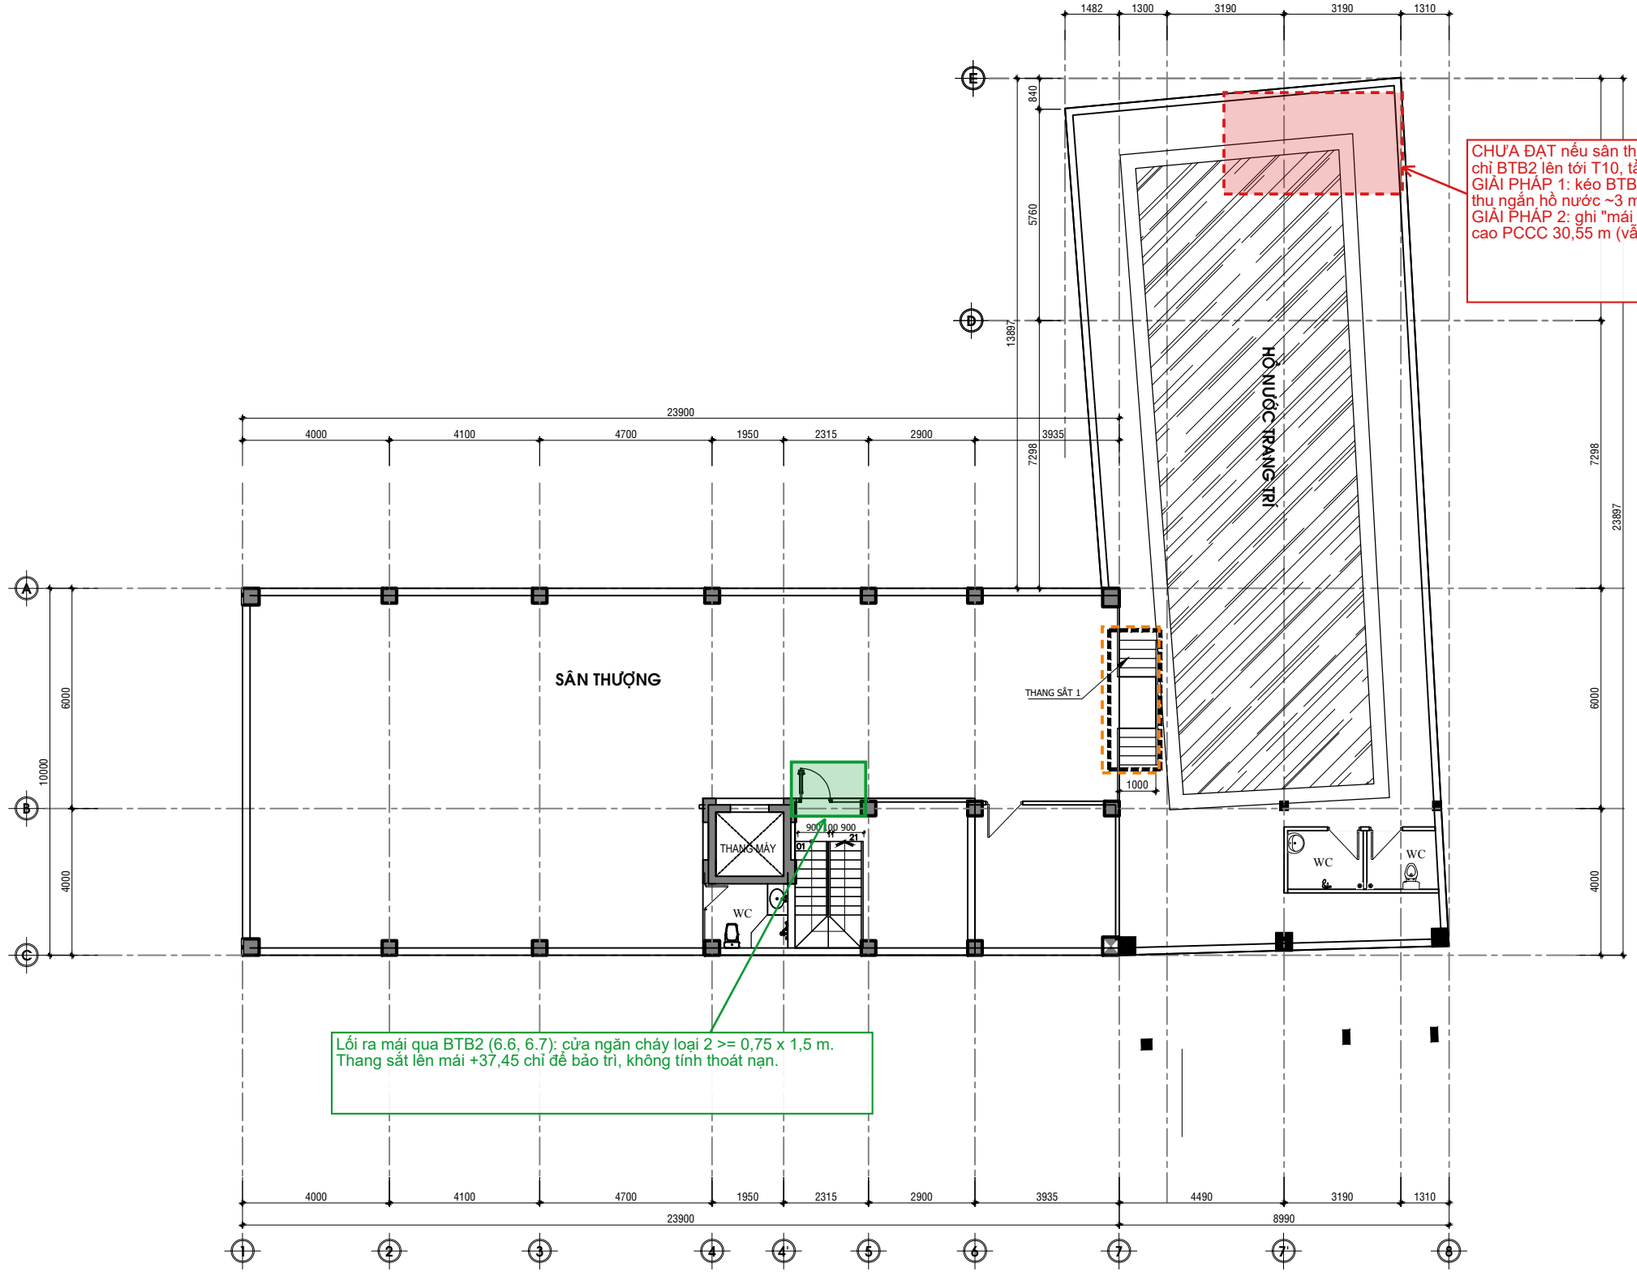

MẶT BẰNG TẦNG 10 TL:1/100

CTY TNHH TƯ VẤN ĐẦU TƯ
CIC
ĐC: VÕ VĂN TÀN - P.TÂN BÌNH
TP ĐỒNG XOÀI - TỈNH BÌNH PHƯỚC
Email: cic.binhphuoc@gmail.com
Tel:0988.600.677
fax: 06513.888.824

GIÁM ĐỐC
Ks. LÊ ĐỨC PHÚC

CHỦ TRÌ
Kts. ĐẶNG CÔNG THÀNH

QUẢN LÝ KỸ THUẬT
Kts. ĐẶNG CÔNG THÀNH

THỂ HIỆN
Kts. ĐẶNG CÔNG THÀNH

CHỦ ĐẦU TƯ
TRẦN VĂN HÙNG


CÔNG TRÌNH
KHÁCH SẠN HOÀNG HÙNG

HẠNG MỤC
KHÁCH SẠN

TÊN BẢN VẼ
MẶT BẰNG SÂN THƯỢNG

TỈ LỆ BV:	1:100	BẢN VẼ TKTC
NGÀY HT:	06/2025	KT:11 /27

TƯ VẤN SƠ BỘ THOÁT NẠN (lần 3, 30/10/2026) – tham khảo, không phải kết luận thẩm định. Chi tiết: tu_van_thiet_ke_v3.md
MẶT ĐỨNG TÂY (trục A-C, hướng bãi đỗ xe chữa cháy): lối vào từ trên cao

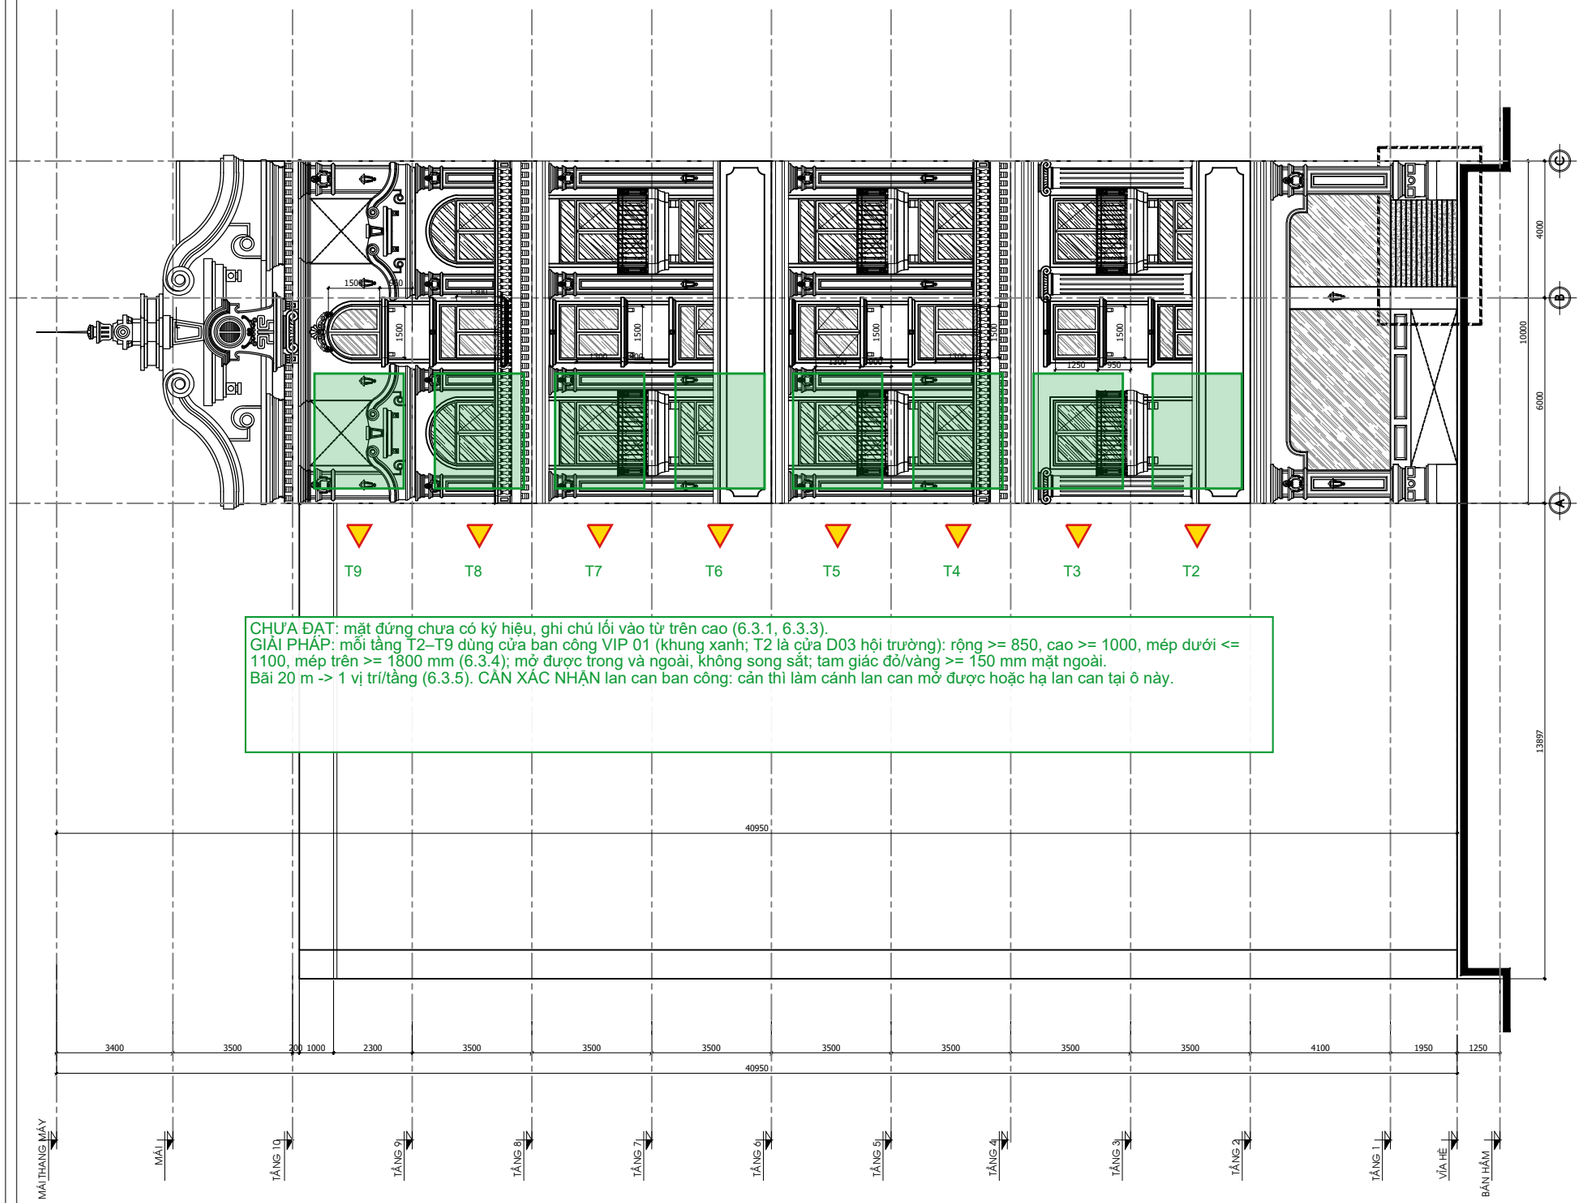

CTY TNHH TƯ VẤN ĐẦU TƯ
CIC
ĐC: VÕ VĂN TÀN - P.TÂN BÌNH
TP ĐỒNG XOÀI - TỈNH BÌNH PHƯỚC
Email: cic.binhphuoc@gmail.com
Tel:0988.600.677
fax: 06513.888.824

GIÁM ĐỐC
Ks. LÊ ĐỨC PHÚC

CHỦ TRÌ
Kts. ĐẶNG CÔNG THÀNH

QUẢN LÝ KỸ THUẬT
Kts. ĐẶNG CÔNG THÀNH

THỂ HIỆN
Kts. ĐẶNG CÔNG THÀNH

CHỦ ĐẦU TƯ
TRẦN VĂN HÙNG

CÔNG TRÌNH
KHÁCH SẠN HOÀNG HÙNG

HẠNG MỤC
KHÁCH SẠN

TÊN BẢN VẼ
MẶT ĐỨNG TRỤC A-C

TỈ LỆ BV:	1:100	BẢN VẼ TKTC
NGÀY HT:	06/2025	KT:13 /27