THIẾT KẾ SƠ BỘ PCCC (tham khảo, chưa phải kết luận thẩm định)
Khách sạn Hoàng Hùng – cao PCCC 34,05 m (> 28 m)

HLLG: 25m từ tim đường

25m

25m

Tim đường vào KCN Minh Hưng III (LG: 5

HLLG: 25m từ tim đường

TIẾP GIÁP NHÀ DÂN

Nhà chỉ có MỘT mặt tiếp giáp đường (mặt Tây, rộng 10 m); Bắc, Nam, Đông giáp nhà dân.
Mọi tiếp cận xe thang/xe bơm phải qua mặt Tây.

9,39m

13,07m

23,94m

26,95m

10m

1

TIẾP GIÁP NHÀ DÂN

27,8m

3500

11m

2

6,99m

14,65m

5,91m

15m

4,36m

12m

HLLG: 6m từ tim đường

Đường BT hiện hữu (LG: 12m)

HLLG: 6m từ tim đường

TIẾP GIÁP NHÀ DÂN

BÃI ĐỖ XE CHỮA CHÁY (đề xuất) 20 x 6 m
- Dài: 1/6 chu vi nhà ≈ 114/6 = 19 m, lấy 20 m (>= 15 m)
- Rộng >= 6 m (Bảng 14, cao PCCC > 15 m)
- Đặt trên đường công cộng (6.2.6), sát lộ giới phía Tây, giữa mặt tiền (trục B)
- Mép gần cách tường ngoài 3,9 m: trong 2–10 m (6.2.3)

Lối phụ phía Đông (rộng 3,5 m từ đường BT 12 m, dài ~26 m < 46 m): chỉ là đường tiếp cận tới cửa Nam sảnh T1 và phòng bơm, KHÔNG đủ rộng làm bãi đỗ (cần >= 6 m).

KÝ HIỆU ĐƯỜNG GIAO THÔNG

**GHI CHÚ:**
**1 - KHÁCH SẠN**
**2 - PHÒNG BƠM VÀ BỂ NƯỚC NGẦM PCCC 140M3**

# MẶT BẰNG TỔNG THỂ L:1/100


CTY TNHH TƯ VẤN ĐẦU TƯ
CIC
ĐC: VÕ VĂN TẦN - P.TÂN BÌNH
TP ĐỒNG XOÀI - TỈNH BÌNH PHƯỚC
Email: cic.binhphuoc@gmail.com
Tel:0988.600.677
fax: 06513.888.824

GIÁM ĐỐC
Ks. LÊ ĐỨC PHÚC

CHỦ TRÌ
Kts. ĐẶNG CÔNG THÀNH

QUẢN LÝ KỸ THUẬT
Kts. ĐẶNG CÔNG THÀNH

THỂ HIỆN
Kts. ĐẶNG CÔNG THÀNH

CHỦ ĐẦU TƯ
TRẦN VĂN HÙNG

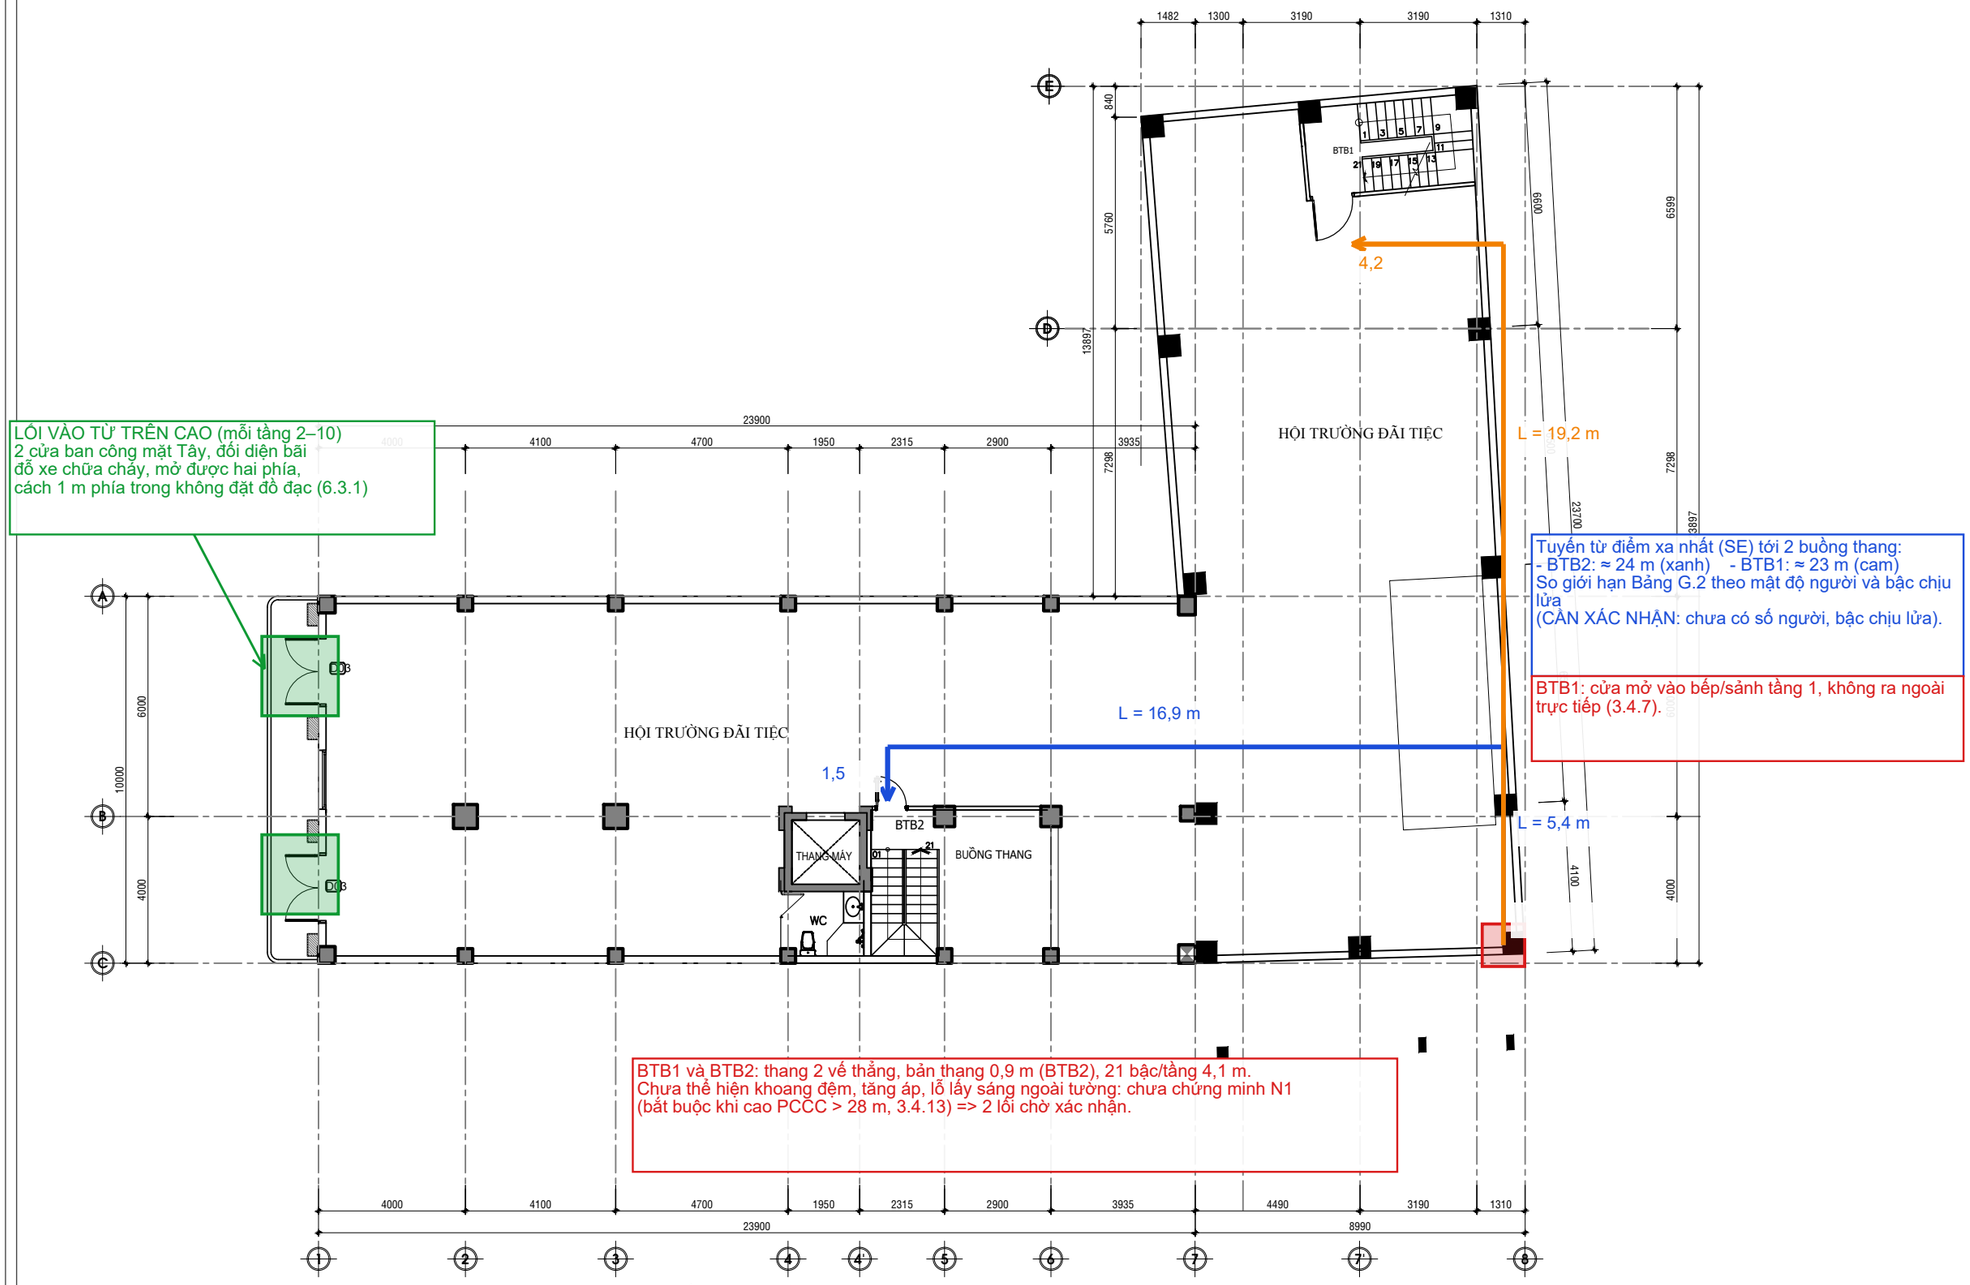

CÔNG TRÌNH
**KHÁCH SẠN HOÀNG HÙNG**

HẠNG MỤC
**KHÁCH SẠN**

TÊN BẢN VẼ
MẶT BẰNG TỔNG THỂ

| TỈ LỆ BV: | 1:100 | BẢN VẼ TKTC |
|---|---|---|
| NGÀY HT: | 06/2025 | KT:01 /27 |

TẦNG 2 (điển hình) – THIẾT KẾ SƠ BỘ PCCC (tham khảo)




MẶT BẰNG TẦNG 2_TL:1/100


CTY TNHH TƯ VẤN ĐẦU TƯ
CIC
ĐC: VÕ VĂN TÀN - P.TÂN BÌNH
TP ĐỒNG XOÀI - TỈNH BÌNH PHƯỚC
Email: cic.binhphuoc@gmail.com
Tel:0988.600.677
fax: 06513.888.824


GIÁM ĐỐC
Ks. LÊ ĐỨC PHÚC

CHỦ TRÌ
Kts. ĐẶNG CÔNG THÀNH

QUẢN LÝ KỸ THUẬT
Kts. ĐẶNG CÔNG THÀNH

THỂ HIỆN
Kts. ĐẶNG CÔNG THÀNH

CHỦ ĐẦU TƯ
TRẦN VĂN HÙNG

CÔNG TRÌNH
**KHÁCH SẠN HOÀNG HÙNG**

HẠNG MỤC
**KHÁCH SẠN**

TÊN BẢN VẼ
MẶT BẰNG TẦNG 2

| TỈ LỆ BV: | 1:100 | BẢN VẼ TKTC |
|---|---|---|
| NGÀY HT: | 06/2025 | KT:05 /27 |