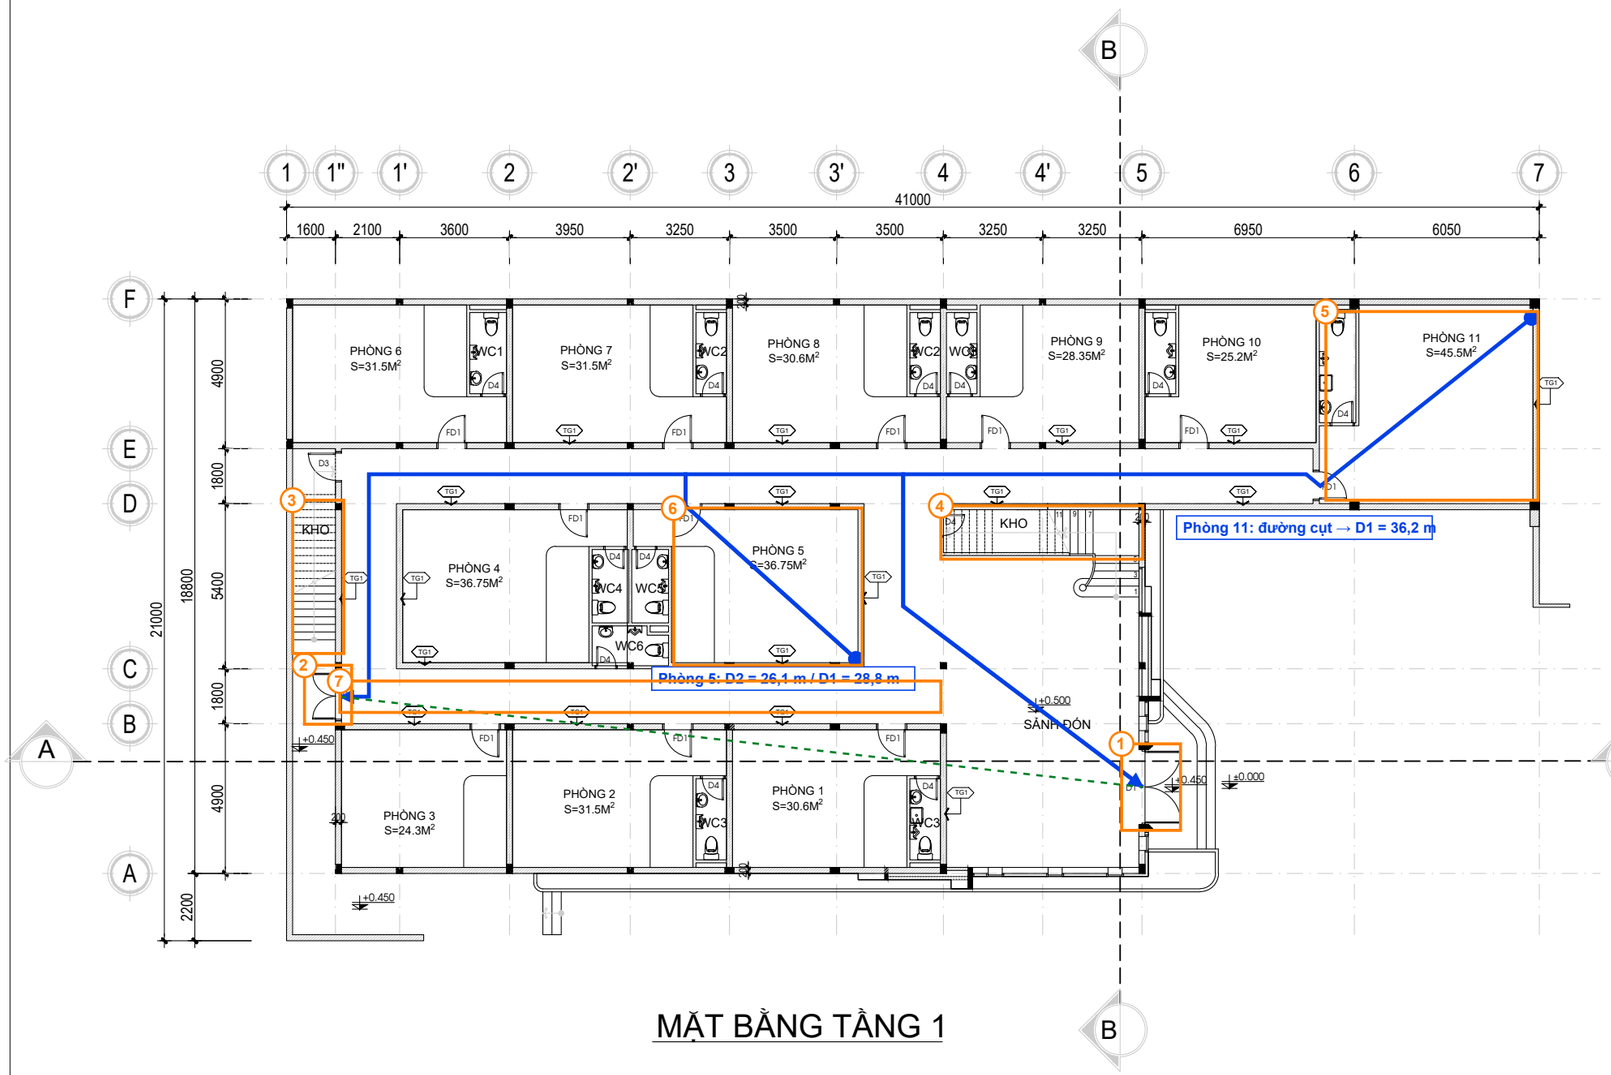


MẶT BẰNG TẦNG 1

KÍ HIỆU	GHI CHÚ	GHCL
D1	CỬA KÍNH 2.45 x 2.4m	-
D2	CỬA KÍNH 1.2 x 2.1m	-
D3	CỬA 0.9 x 2.1m	-
D4	CỬA 0.8 x 1.9m	-
FD1	CỬA THOÁT HIỂM 0.9 x 2.1m	EI60
W1	VÁCH KÍNH	-
W2	Ô KÍNH LẤY SÁNG 1 x 1.4m	-
W3	CỬA SỔ 0.9 x 1m	-
W4	Ô KÍNH LẤY SÁNG 0.8 x 1.5m	-
W5	Ô KÍNH LẤY SÁNG 2 x 0.3m	-

GHI CHÚ ĐƯỜNG THOÁT NẠN – TẦNG 1

1. D1 (cửa chính) – theo xác nhận của người thẩm định được coi là lối thoát nạn tầng 1 (L1). NGHI VẤN: bản vẽ chưa ghi chú 'lối thoát nạn' trên cửa → cần bổ sung ghi chú.
2. D2 (cạnh chân thang CT1) – theo xác nhận được coi là lối thoát nạn tầng 1 (L2). NGHI VẤN: cũng chưa ghi chú thoát nạn trên bản vẽ → cần bổ sung ghi chú/đối ký hiệu cửa.
3. Phòng KHO nằm DƯỚI thang thoát hiểm CT1 (cửa D3) → NGHI VẤN: không nên bố trí kho/vật liệu cháy dưới thang thoát nạn.
4. KHO dưới thang sảnh (cửa D4) – nếu thang sảnh là CT2 thì cũng lưu ý như mục 3.
5. Đường cụt: điểm xa nhất Phòng 11 → D1 = 36,2 m (ước lượng). Giới hạn cho phép cần tra QCVN 06; bản vẽ không có bảng tính.
6. Giữa 2 lối: điểm xa nhất Phòng 5 → D2 = 26,1 m, → D1 = 28,8 m (ước lượng).
7. Phân tán 2 lối: L(D2–D1) ≈ 26,4 m ≥ ½D = 14,5 m và ≥ ½D = 21,7 m (D ≈ 43,5 m) → ĐẠT.
8. Chú giải CT1/CT2 (thang thoát nạn số 01, 02) không có ký hiệu CT1/CT2 trên mặt bằng; cửa FD1 ghi 'cửa thoát hiểm' nhưng gắn cho cửa phòng → nên ký hiệu rõ lối thoát nạn và vị trí CT1, CT2 trên từng tầng.

Ghi chú chung

Mũi tên xanh = đường thoát nạn từ điểm xa nhất trong phòng tới D1/D2 (D1, D2 coi là lối thoát nạn theo xác nhận, chưa ghi chú trên bản vẽ). Chiều dài đo theo trục tim hành lang, ước lượng theo tỉ lệ trục 41000 mm, sai số ±1–2 m.

Có Sprinkler (ghi chú mặt đứng trang 6, 7) → dùng ⅓D; ½D nêu để tham khảo.


TG1 : TƯỜNG GẠCH DÀY 200MM, XÂY CAO TỚI ĐÁY SÀN TRÁT 2 MẶT XI MĂNG CÁT .

TG2 : TƯỜNG GẠCH DÀY 100MM, XÂY CAO TỚI ĐÁY SÀN TRÁT 2 MẶT XI MĂNG CÁT.

8 CT1: THANG THOÁT NẠN SỐ 01
CT2: THANG THOÁT NẠN SỐ 02

Nhà Karaoke có bậc chịu lửa bậc II, cấp nguy hiểm cháy S0:

- Cột chịu lực và các bộ phận chịu lực khác: R90
=> Thiết kế dầm, cột BTCT GHCL R90
- Tường ngoài không chịu lực: E15
=> Thiết kế tường gạch dày 200mm, GHCL REI 150 cao đến mái.
- Sàn tầng: REI45
=> Thiết kế sàn BTCT dày 100mm, GHCL REI 45.
- Kết cấu mái: BTCT
* Công trình có cấp nguy hiểm cháy S0 theo bảng 5 QCVN 06:2022/BXD như sau:
- Cột chịu lực có cấp nguy hiểm cháy K0.
- Tường ngoài là tường gạch 200mm có cấp nguy hiểm cháy K0.

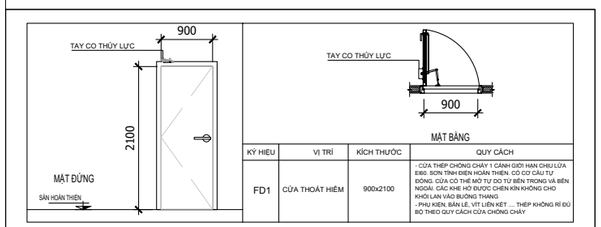

CHI TIẾT CỬA CHỐNG CHÁY-FD1

CHIẾU SÁNG THANG BỘ TRONG NHÀ (THEO ĐIỀU MỤC a, ĐIỀU 3.4.8 CỦA SỬA ĐỔI 1:2023 QCVN 06:2022/BXD):
+ TRỪ BUỒNG THANG BỘ LOẠI L2 VÀ PHẦN CẦU THANG TẠI TẦNG HẦM, TẦNG BÁN HẦM, VIỆC ĐẢM BẢO CHIẾU SÁNG CÓ THỂ ĐƯỢC THỰC HIỆN BẰNG CÁC LỖ LẤY ÁNH SÁNG VỚI DIỆN TÍCH KHÔNG NHỎ HƠN 1,2 M2 TRÊN CÁC TƯỜNG NGOÀI Ở MỖI TẦNG

BẢNG THỐNG KÊ

NỘI DUNG	HẠNG MỤC	GHI CHÚ
CÔNG NĂNG	KARAOKE	BẢNG H.2 BẢNG H.7 MỤC H.2.12.10 PHỤ LỤC H SỬA ĐỔI 01:2023 QC06/2022-BXD
NHÓM NHÀ	F2.1	
DIỆN TÍCH (M2)	595	
SỐ TẦNG	02	
CHIỀU CAO PCCC (M)	7.7	
CHIỀU CAO MÁI (M)	8.9	
KHỐI TÍCH (M3)	4938.5	
BẬC CHỊU LỬA	II	
CẤP NGUY HIỂM CHÁY	S0	
SỐ LƯỢNG NGƯỜI LỚN NHẤT	93	

MỤC ĐÍCH PHÁT HÀNH / ISSUED FOR

- ☐ THÔNG TIN / FOR INFORMATION
- ☐ DỰ TOÁN / FOR ESTIMATE
- ☑ CHẤP THUẬN / FOR APPROVAL
- ☐ ĐẤU THẦU / FOR TENDER
- ☐ ĐIỀU CHỈNH / FOR RESUBMISSION

CHỦ ĐẦU TƯ

HỘ KINH DOANH KARAOKE HOÀNG ANH

ĐƠN VỊ TƯ VẤN THIẾT KẾ XÂY DỰNG

CÔNG TY TNHH ĐẦU TƯ & PHÁT TRIỂN THƯƠNG MẠI DỊCH VỤ KIẾN TRUNG

KIẾN TRUNG

Địa chỉ: Số 310, Quốc lộ 1A, Khu phố 3, Phường Tam Bình, TP. Thủ Đức, TP. Hồ Chí Minh
Điện thoại: 0967 000 485

GIÁM ĐỐC

PHẠM THANH QUANG

CHỦ TRÌ & THIẾT KẾ:

ĐẶNG QUỐC THÁI

THỂ HIỆN:

NGUYỄN PHÚ TOÀN

TÊN DỰ ÁN

KARAOKE HOÀNG ANH 2 & CÁC CÔNG TRÌNH PHỤ TRỢ


ĐỊA CHỈ: TDS 305, 306, 886, 519 VÀ 842, TBĐS 8, PHƯỜNG TÂN PHƯỚC KHÁNH,TP. TÂN UYÊN, TỈNH BÌNH DƯƠNG

TÊN BẢN VẼ

MẶT BẰNG TẦNG 1

HẠNG MỤC

KÍ HIỆU.BV	NGÀY HOÀN THÀNH
KT-02	Tháng 12/2024

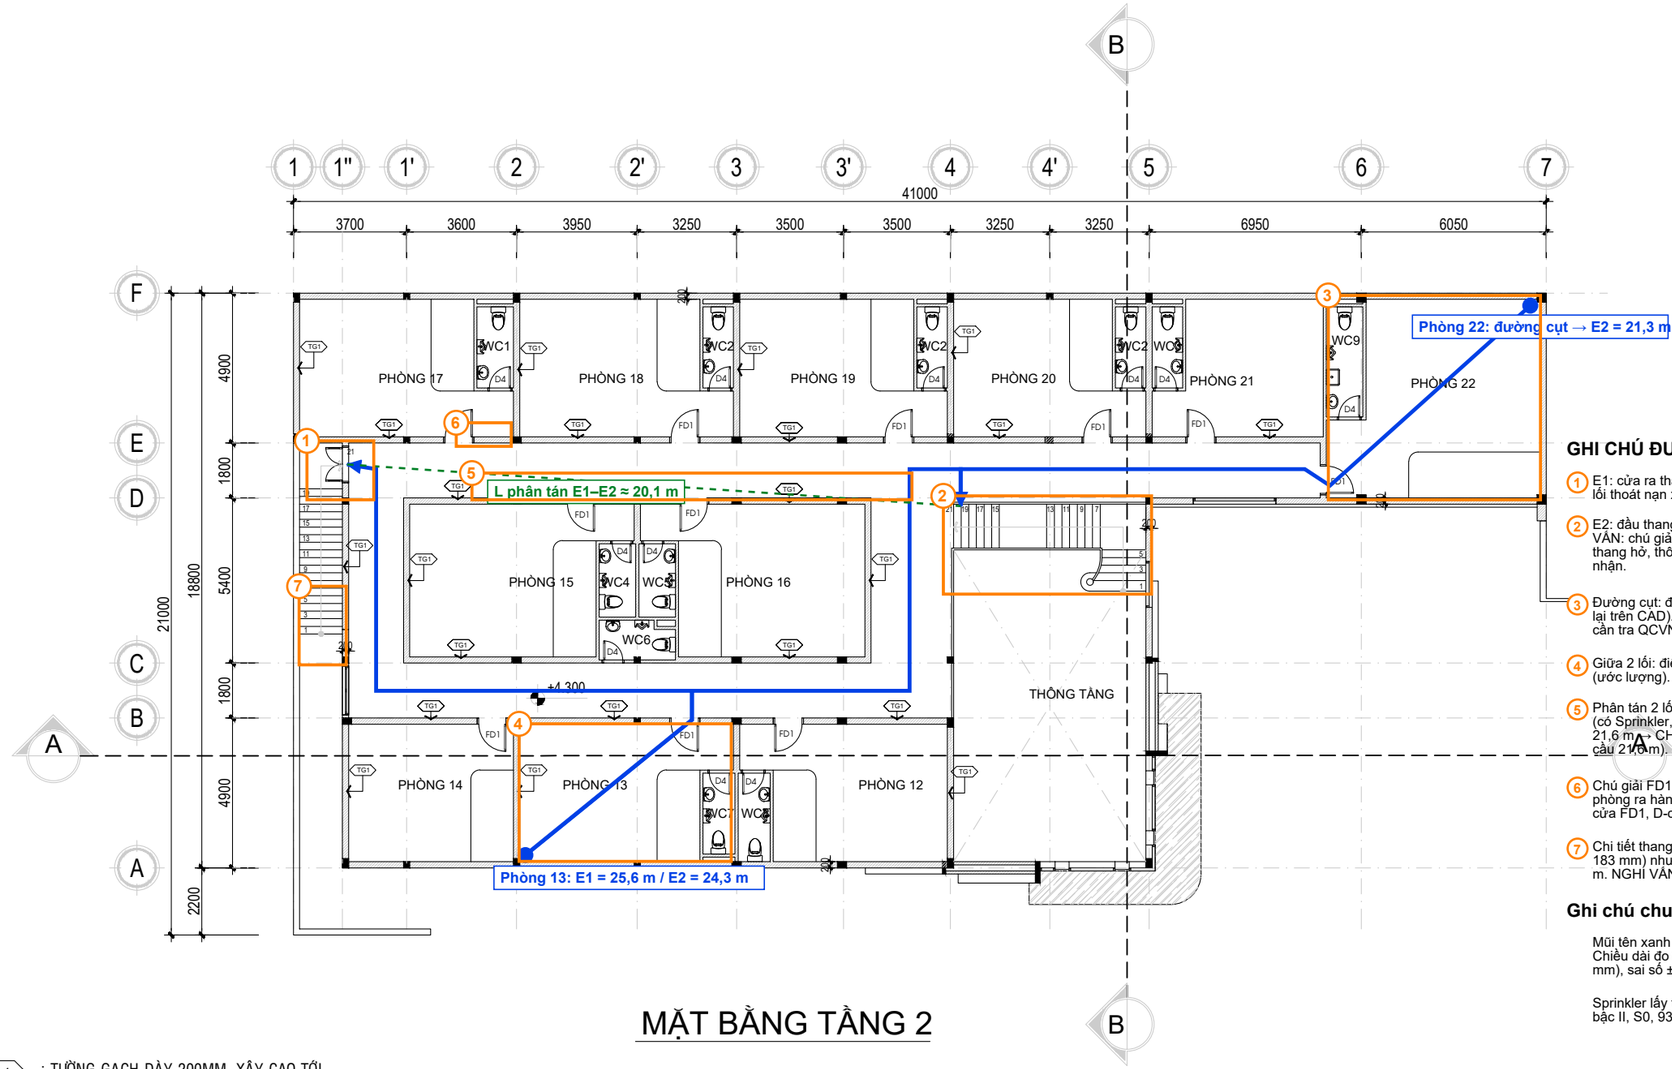

MẶT BẰNG TẦNG 2


TG1 : TƯỜNG GẠCH DÀY 200MM, XÂY CAO TỚI ĐÁY SÀN TRÁT 2 MẶT XI MĂNG CÁT .

TG2 : TƯỜNG GẠCH DÀY 100MM, XÂY CAO TỚI ĐÁY SÀN TRÁT 2 MẶT XI MĂNG CÁT.

CT1: THANG THOÁT NẠN SỐ 01
CT2: THANG THOÁT NẠN SỐ 02

Nhà Karaoke có bậc chịu lửa bậc II, cấp nguy hiểm cháy S0:

- Cột chịu lực và các bộ phận chịu lực khác: R90
=> Thiết kế dầm, cột BTCT GHCL R90
- Tường ngoài không chịu lực: E15
=> Thiết kế tường gạch dày 200mm, GHCL REI 150 cao đến mái.
- Sàn tầng: REI45
=> Thiết kế sàn BTCT dày 100mm, GHCL REI 45.
- Kết cấu mái: BTCT
* Công trình có cấp nguy hiểm cháy S0 theo bảng 5 QCVN 06:2022/BXD như sau:
- Cột chịu lực có cấp nguy hiểm cháy K0.
- Tường ngoài là tường gạch 200mm có cấp nguy hiểm cháy K0.

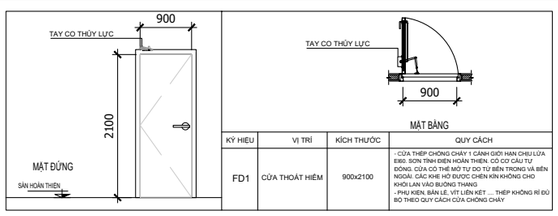

CHI TIẾT CỬA CHỐNG CHÁY-FD1

CHIẾU SÁNG THANG BỘ TRONG NHÀ (THEO ĐIỀU MỤC a, ĐIỀU 3.4.8 CỦA SỬA ĐỔI 1:2023 QCVN 06:2022/BXD):
+ TRỪ BUỒNG THANG BỘ LOẠI L2 VÀ PHẦN CẦU THANG TẠI TẦNG HẦM, TẦNG BÁN HẦM, VIỆC ĐẢM BẢO CHIẾU SÁNG CÓ THỂ ĐƯỢC THỰC HIỆN BẰNG CÁC LỖ LẤY ÁNH SÁNG VỚI DIỆN TÍCH KHÔNG NHỎ HƠN 1,2 M2 TRÊN CÁC TƯỜNG NGOÀI Ở MỖI TẦNG

GHI CHÚ ĐƯỜNG THOÁT NẠN – TẦNG 2

1. E1: cửa ra thang thoát hiểm ngoài nhà CT1 (thang thoát nạn số 01) – lối thoát nạn xác định được. Dùng làm lối thoát tầng 2.
2. E2: đầu thang sảnh – GIẢ ĐỊNH là CT2 (thang thoát nạn số 02). NGHI VẤN: chú giải CT1/CT2 không ký hiệu lên mặt bằng; thang sảnh là thang hở, thông tầng, không phải buồng thang ngăn cháy. Cần xác nhận.
3. Đường cụt: điểm xa nhất Phòng 22 → E2 = 21,3 m (ước lượng, cần đo lại trên CAD). Bản vẽ không có bảng tính chiều dài; giới hạn cho phép cần tra QCVN 06 (F2.1, bậc II, S0).
4. Giữa 2 lối: điểm xa nhất Phòng 13 → E1 = 25,6 m, → E2 = 24,3 m (ước lượng). Cần đối chiếu giới hạn QCVN 06.
5. Phân tán 2 lối: L(E1–E2) ≈ 20,1 m (≥ 7 m). D ≈ 43,2 m → ½D = 14,4 m (có Sprinkler, ghi ở mặt đứng) → ĐẠT. Nếu không tính Sprinkler: ½D = 21,6 m → CHƯA ĐẠT (Khoảng cách thiết kế 20,1 m bé hơn số liệu yêu cầu 21,6m). Sát giới hạn.
6. Chú giải FD1 ghi 'Cửa thoát hiểm EI60' nhưng dùng cho cửa của MỌI phòng ra hành lang → nghi ghi nhầm / không phải lối ra thoát nạn. Các cửa FD1, D-cửa khác KHÔNG tính là lối thoát.
7. Chi tiết thang thoát hiểm (trang 11): cao độ -0,050 → +3,800 (21 bậc × 183 mm) nhưng sàn tầng 2 = +4,300 (mặt đứng/mặt bằng) → lệch ~0,5 m. NGHI VẤN thiết kế thang.

Ghi chú chung

Mũi tên xanh = đường thoát nạn tính từ điểm xa nhất trong phòng. Chiều dài đo theo trục tim hành lang, ước lượng từ tỉ lệ trục (41000 mm), sai số ±1–2 m.

Sprinkler lấy từ ghi chú mặt đứng trục A-F / 1-7 (trang 6, 7); nhóm F2.1, bậc II, S0, 93 người theo bảng thống kê.

BẢNG THỐNG KÊ

NỘI DUNG	HẠNG MỤC	GHI CHÚ
CÔNG NĂNG	KARAOKE	BẢNG H.2 BẢNG H.7 MỤC H.2.12.10 PHỤ LỤC H SỬA ĐỔI 01:2023 QC06/2022-BXD
NHÓM NHÀ	F2.1	
DIỆN TÍCH (M2)	595	
SỐ TẦNG	02	
CHIỀU CAO PCCC (M)	7.7	
CHIỀU CAO MÁI (M)	8.9	
KHỐI TÍCH (M3)	4938.5	
BẬC CHỊU LỬA	II	
CẤP NGUY HIỂM CHÁY	S0	
SỐ LƯỢNG NGƯỜI LỚN NHẤT	93	

MỤC ĐÍCH PHÁT HÀNH / ISSUED FOR

- ☐ THÔNG TIN / FOR INFORMATION
- ☐ DỰ TOÁN / FOR ESTIMATE
- ☒ CHẤP THUẬN / FOR APPROVAL
- ☐ ĐẤU THẦU / FOR TENDER
- ☐ ĐIỀU CHỈNH / FOR RESUBMISSION

CHỦ ĐẦU TƯ

HỘ KINH DOANH KARAOKE HOÀNG ANH

ĐƠN VỊ TƯ VẤN THIẾT KẾ XÂY DỰNG

CÔNG TY TNHH ĐẦU TƯ & PHÁT TRIỂN THƯƠNG MẠI DỊCH VỤ KIẾN TRUNG

KIẾN TRUNG

Địa chỉ: Số 310, Quốc lộ 1A, Khu phố 3, Phường Tam Bình, TP. Thủ Đức, TP. Hồ Chí Minh
Điện thoại: 0967 000 485

GIÁM ĐỐC

PHẠM THANH QUANG

CHỦ TRÌ & THIẾT KẾ:

ĐẶNG QUỐC THÁI

THỂ HIỆN:

NGUYỄN PHÚ TOÀN

TÊN DỰ ÁN

KARAOKE HOÀNG ANH 2 & CÁC CÔNG TRÌNH PHỤ TRỢ

ĐỊA CHỈ: TDS 305, 306, 886, 519 VÀ 842, TBĐS 8, PHƯỜNG TÂN PHƯỚC KHÁNH,TP. TÂN UYÊN, TỈNH BÌNH DƯƠNG

TÊN BẢN VẼ

MẶT BẰNG TẦNG 2

HẠNG MỤC

KÍ HIỆU.BV	NGÀY HOÀN THÀNH
KT-02	Tháng 12/2024