
GHI CHÚ THẨM ĐỊNH (khung đánh số trên bản vẽ)

13. [CHỈNH BẢN VẼ] Bổ sung ghi chú chiều cao PCCC 7,6 m trên mặt đứng (Đ.1.4.9).

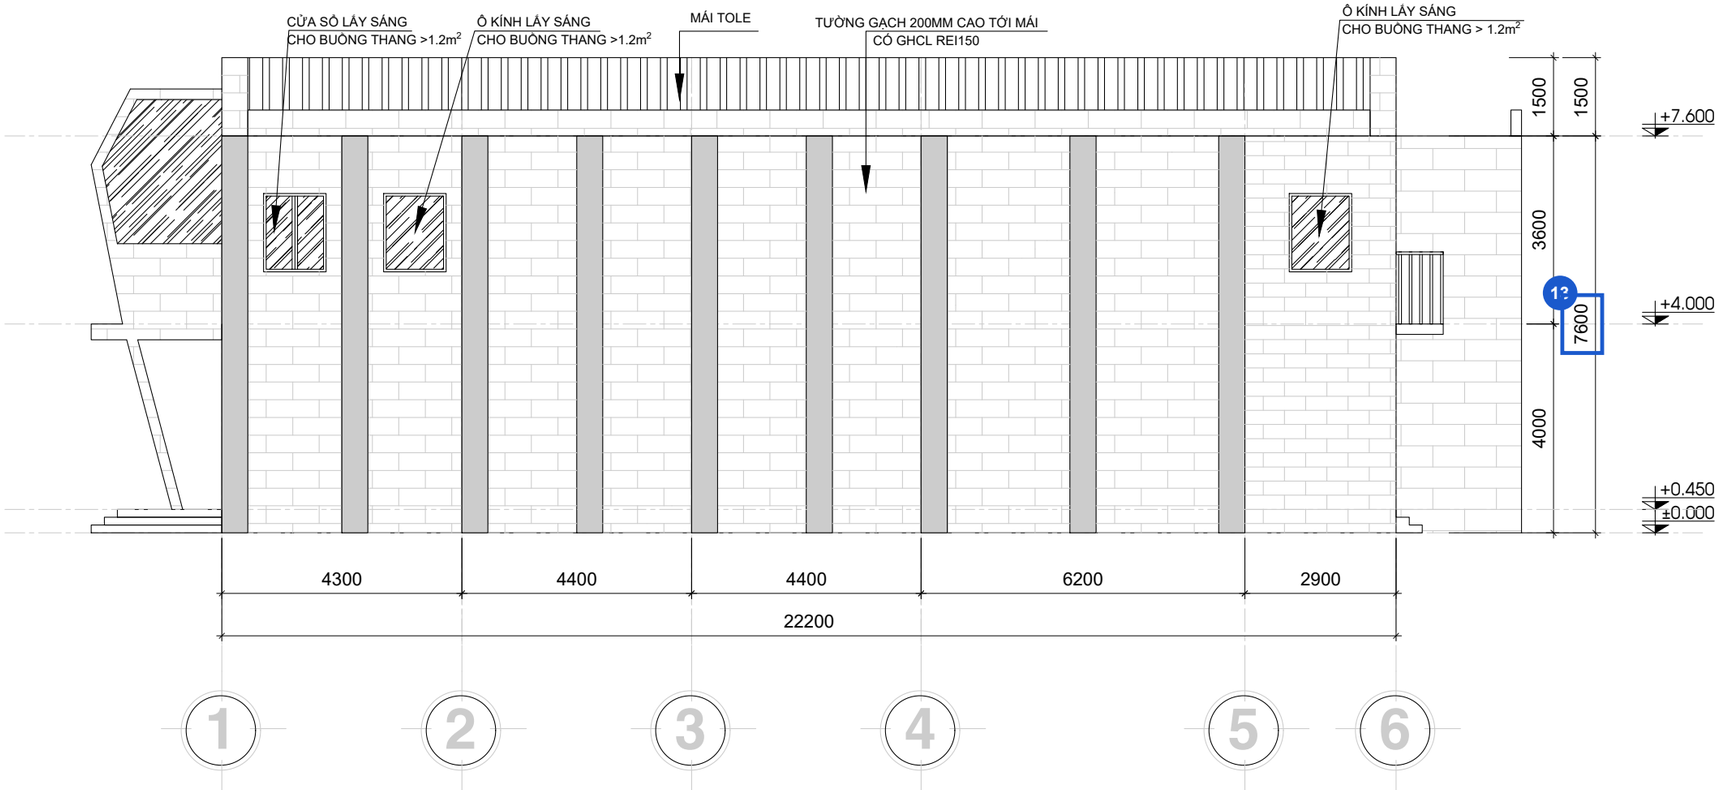

MẶT ĐỨNG CẢI TẠO 1-6 KARAOKE

Mặt đứng 1-6 của Karaoke cách đường cách đường ranh giới khu đất 5.6 >3m nên không quy định tỉ lệ tổng diện tích các lỗ mở không được bảo vệ chống cháy so với tổng diện tích bề mặt tường trục 1-6
Mặt đứng 1-6 của Karaoke là tường gạch 200mm GHCL REI150
Công trình được bảo vệ bằng hệ thống chữa cháy sprinkler nên không yêu cầu giải pháp ngăn cháy theo phương đứng theo (Đ.4.33.1 đến Đ.4.33.3 Sửa đổi 01:2023 QCVN06/2022-BXD)

MỤC ĐÍCH PHÁT HÀNH / ISSUED FOR

☐	THÔNG TIN / FOR INFORMATION
☐	DỰ TOÁN / FOR ESTIMATE
☒	CHẤP THUẬN / FOR APPROVAL
☐	ĐẤU THẦU / FOR TENDER
☐	ĐIỀU CHỈNH / FOR RESUBMISSION

CHỦ ĐẦU TƯ

HỘ KINH DOANH KARAOKE HOÀNG ANH

TĐS 14, TBĐS 30, PHƯỜNG TÂN PHƯỚC KHÁNH, TP. TÂN UYÊN, TỈNH BÌNH DƯƠNG

ĐƠN VỊ TƯ VẤN THIẾT KẾ XÂY DỰNG

CÔNG TY TNHH ĐẦU TƯ & PHÁT TRIỂN THƯƠNG MẠI DỊCH VỤ KIẾN TRUNG

KIẾN TRUNG

Địa chỉ: Số 310, Quốc lộ 1A, Khu phố 3, Phường Tam Bình, TP. Thủ Đức, TP. Hồ Chí Minh
Điện thoại: 0967 000 485

GIÁM ĐỐC

PHẠM THANH QUANG

CHỦ TRÌ & THIẾT KẾ:

ĐẶNG QUỐC THÁI

THỂ HIỆN:

NGUYỄN PHÚ TOÀN

TÊN DỰ ÁN

CẢI TẠO KARAOKE HOÀNG ANH

TĐS 14, TBĐS 30, PHƯỜNG TÂN PHƯỚC KHÁNH, TP. TÂN UYÊN, TỈNH BÌNH DƯƠNG

TÊN BẢN VẼ

MẶT ĐỨNG CẢI TẠO 1-6 KARAOKE


HẠNG MỤC

KIẾN TRÚC

KÍ HIỆU.BV	NGÀY HOÀN THÀNH
KT-10	Tháng 12/2024

GHI CHÚ THẨM ĐỊNH (khung đánh số trên bản vẽ)

13. [CHỈNH BẢN VẼ] Bổ sung ghi chú chiều cao PCCC 7,6 m trên mặt đứng (Đ.1.4.9).

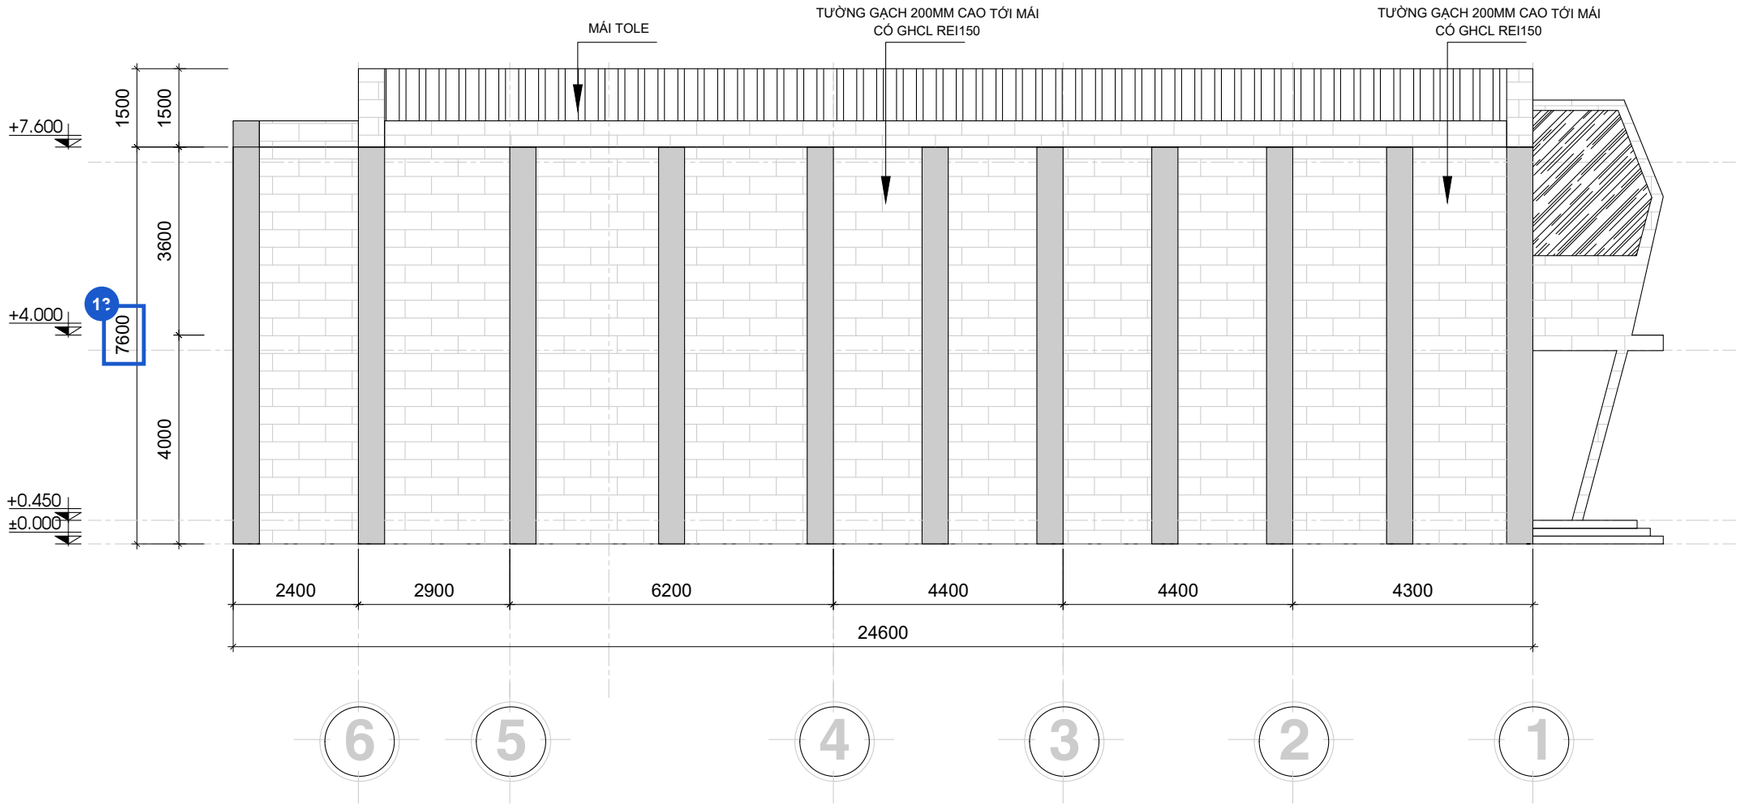

MẶT ĐỨNG CẢI TẠO 6-1 KARAOKE

Mặt đứng 6-4 của Karaoke cách đường cách phòng nhân viên và bếp 0.75m < 3m.
Theo bảng E.1 Sửa đổi 01:2023 QCVN06/2022-BXD khoảng cách phòng cháy chống cháy giữa các nhà ở, nhà và công trình công cộng:
- Phòng nhân viên có bậc chịu lửa bậc II, cấp S0
- Karaoke có bậc chịu lửa bậc II, cấp S0
=> Mặt đứng 6-4 của Karaoke xây tường gạch 200mm xây cao tới mái, không mở các ô cửa sổ.
Mặt đứng 4-1 của Karaoke là tường gạch 200mm GHCL REI150
Công trình được bảo vệ bằng hệ thống chữa cháy sprinkler nên không yêu cầu giải pháp ngăn cháy theo phương đứng theo (Đ.4.33.1 đến Đ.4.33.3 Sửa đổi 01:2023 QCVN06/2022-BXD)

MỤC ĐÍCH PHÁT HÀNH / ISSUED FOR

☐	THÔNG TIN / FOR INFORMATION
☐	DỰ TOÁN / FOR ESTIMATE
☒	CHẤP THUẬN / FOR APPROVAL
☐	ĐẤU THẦU / FOR TENDER
☐	ĐIỀU CHỈNH / FOR RESUBMISSION

CHỦ ĐẦU TƯ

HỘ KINH DOANH KARAOKE HOÀNG ANH

TĐS 14, TBĐS 30, PHƯỜNG TÂN PHƯỚC KHÁNH, TP. TÂN UYÊN, TỈNH BÌNH DƯƠNG

ĐƠN VỊ TƯ VẤN THIẾT KẾ XÂY DỰNG

CÔNG TY TNHH ĐẦU TƯ & PHÁT TRIỂN THƯƠNG MẠI DỊCH VỤ KIẾN TRUNG

KIẾN TRUNG

Địa chỉ: Số 310, Quốc lộ 1A, Khu phố 3, Phường Tam Bình, TP. Thủ Đức, TP. Hồ Chí Minh
Điện thoại: 0967 000 485

GIÁM ĐỐC

PHẠM THANH QUANG

CHỦ TRÌ & THIẾT KẾ:

ĐẶNG QUỐC THÁI

THỂ HIỆN:

NGUYỄN PHÚ TOÀN

TÊN DỰ ÁN

CẢI TẠO KARAOKE HOÀNG ANH

TĐS 14, TBĐS 30, PHƯỜNG TÂN PHƯỚC KHÁNH, TP. TÂN UYÊN, TỈNH BÌNH DƯƠNG

TÊN BẢN VẼ

MẶT ĐỨNG CẢI TẠO 6-1 KARAOKE


HẠNG MỤC

KIẾN TRÚC

KÍ HIỆU.BV	NGÀY HOÀN THÀNH
KT-11	Tháng 12/2024


GHI CHÚ THẨM ĐỊNH (khung đánh số trên bản vẽ)

13. [CHỈNH BẢN VẼ] Bổ sung ghi chú chiều cao PCCC 7,6 m trên mặt đứng (Đ.1.4.9).

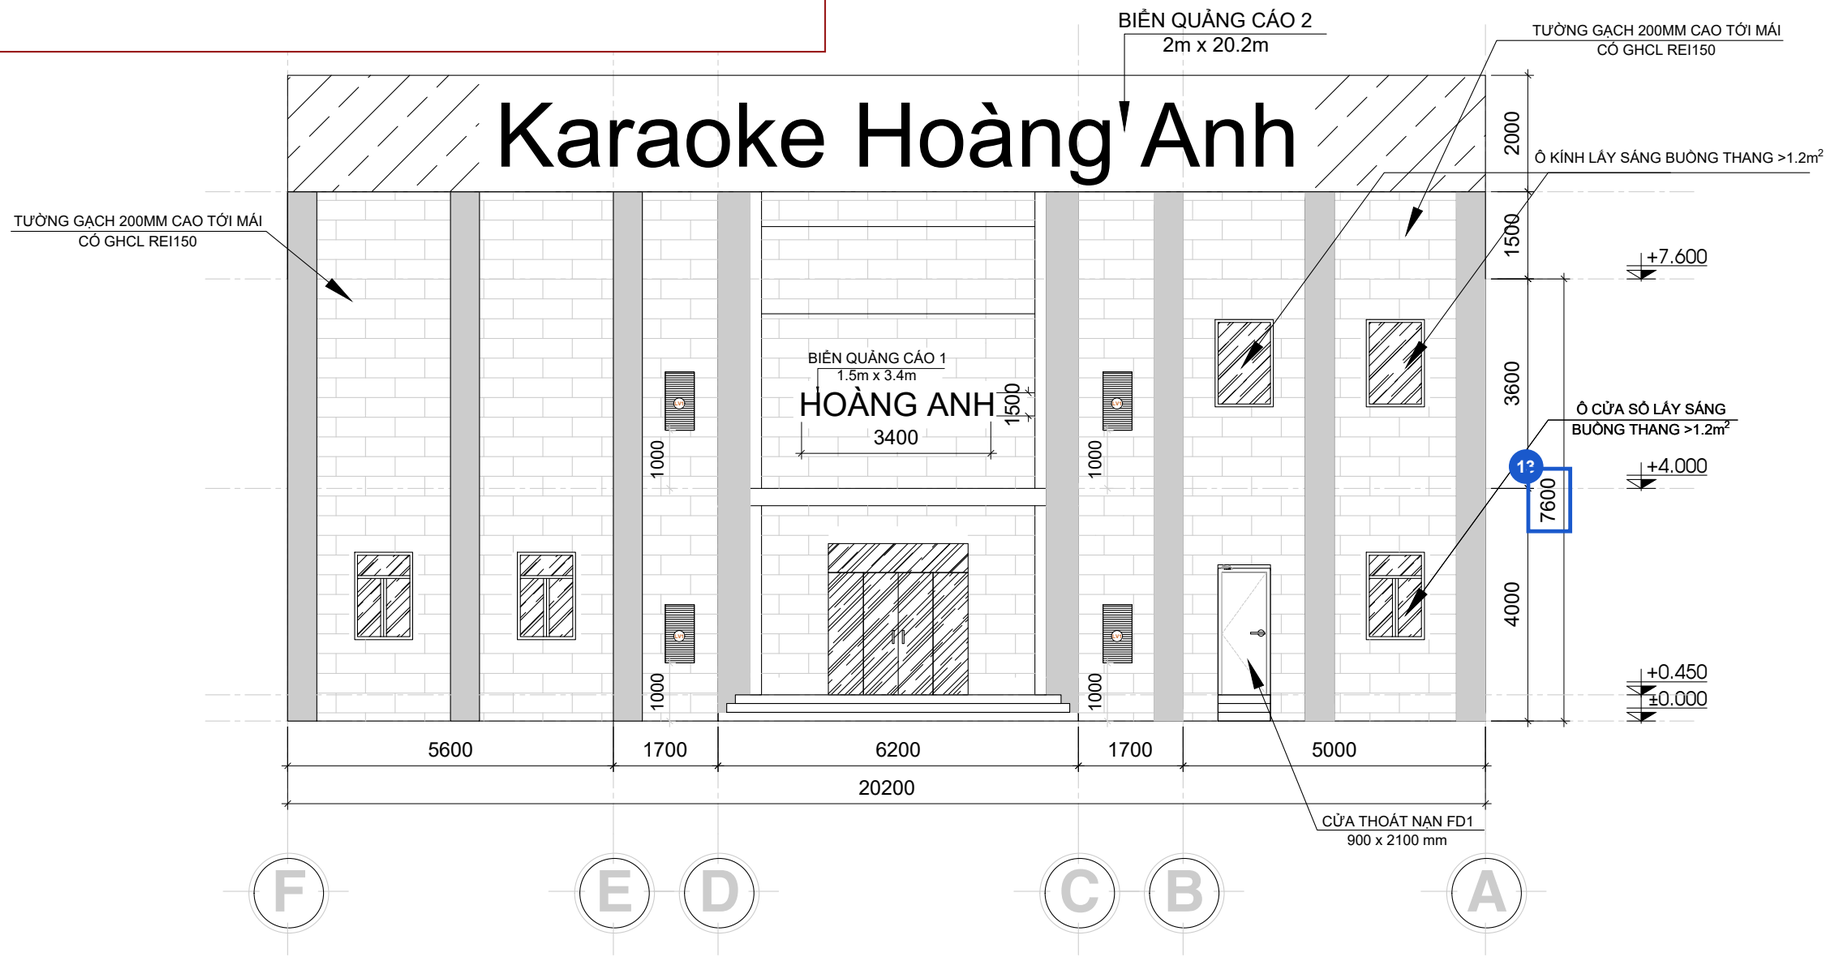

MẶT ĐỨNG CẢI TẠO F-A KARAOKE

Mặt đứng F-A của Karaoke cách đường cách đường ranh giới khu đất 17m >3m nên không quy định tỉ lệ tổng diện tích các lỗ mở không được bảo vệ chống cháy so với tổng diện tích bề mặt tường trục F-A
Công trình được bảo vệ bằng hệ thống chữa cháy sprinkler nên không yêu cầu giải pháp ngăn cháy theo phương đứng theo (Đ.4.33.1 đến Đ.4.33.3 Sửa đổi 01:2023 QCVN06/2022-BXD)

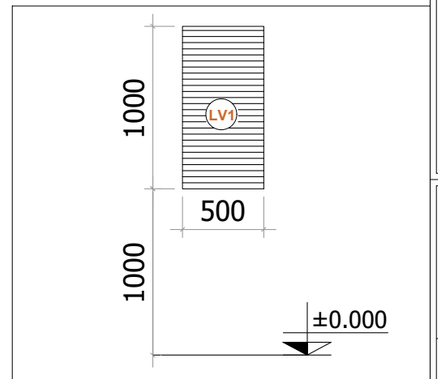

LOUVER BÙ KHÍ TỰ NHIÊN (SL : 4)
KÍCH THƯỚC 500x1000mm

MỤC ĐÍCH PHÁT HÀNH / ISSUED FOR

- ☐ THÔNG TIN / FOR INFORMATION
- ☐ DỰ TOÁN / FOR ESTIMATE
- ☒ CHẤP THUẬN / FOR APPROVAL
- ☐ ĐẤU THẦU / FOR TENDER
- ☐ ĐIỀU CHỈNH / FOR RESUBMISSION

CHỦ ĐẦU TƯ

HỘ KINH DOANH KARAOKE HOÀNG ANH
TĐS 14, TBĐS 30, PHƯỜNG TÂN PHƯỚC KHÁNH, TP. TÂN UYÊN, TỈNH BÌNH DƯƠNG

ĐƠN VỊ TƯ VẤN THIẾT KẾ XÂY DỰNG

CÔNG TY TNHH ĐẦU TƯ & PHÁT TRIỂN THƯƠNG MẠI DỊCH VỤ KIẾN TRUNG

KIẾN TRUNG

Địa chỉ: Số 310, Quốc lộ 1A, Khu phố 3, Phường Tam Bình, TP. Thủ Đức, TP. Hồ Chí Minh
Điện thoại: 0967 000 485

GIÁM ĐỐC

PHẠM THANH QUANG

CHỦ TRÌ & THIẾT KẾ:

ĐẶNG QUỐC THÁI

THỂ HIỆN:

NGUYỄN PHÚ TOÀN

TÊN DỰ ÁN

CẢI TẠO KARAOKE HOÀNG ANH

TĐS 14, TBĐS 30, PHƯỜNG TÂN PHƯỚC KHÁNH, TP. TÂN UYÊN, TỈNH BÌNH DƯƠNG

TÊN BẢN VẼ


MẶT ĐỨNG CẢI TẠO F-A KARAOKE

HẠNG MỤC
KIẾN TRÚC

KÍ HIỆU.BV	NGÀY HOÀN THÀNH
KT-12	Tháng 12/2024

GHI CHÚ THẨM ĐỊNH (khung đánh số trên bản vẽ)

13. [CHỈNH BẢN VẼ] Bổ sung ghi chú chiều cao PCCC 7,6 m trên mặt đứng (Đ.1.4.9).

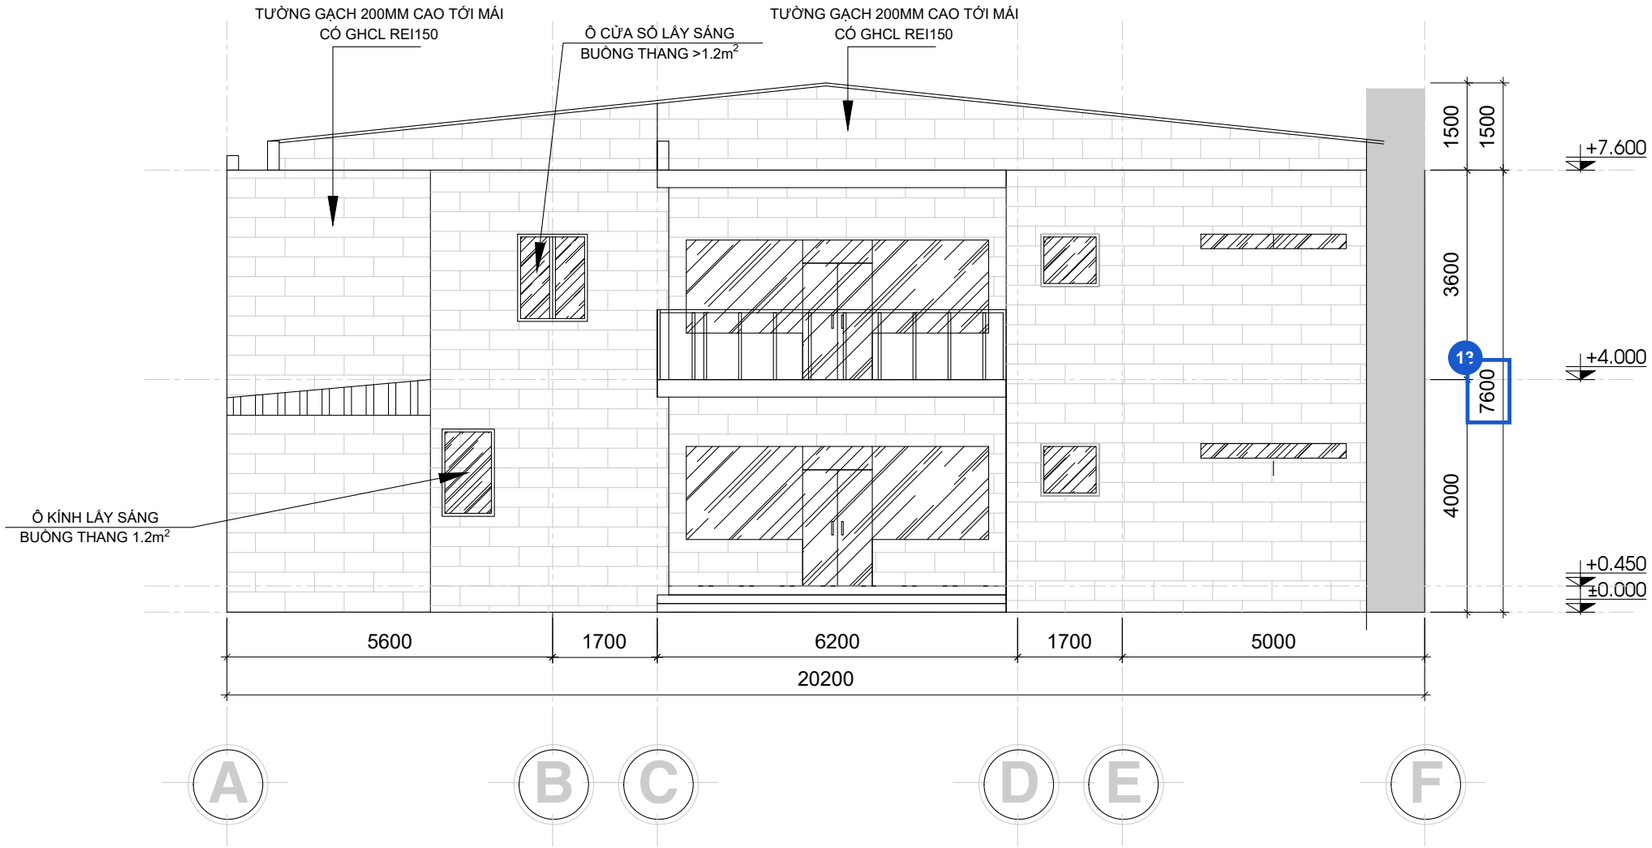

MẶT ĐỨNG CẢI TẠO A-F KARAOKE

Mặt đứng A-F của Karaoke cách đường quy ước >3m nên không quy định tỉ lệ tổng diện tích các lỗ mở không được bảo vệ chống cháy so với tổng diện tích bề mặt tường trục A-F

Công trình được bảo vệ bằng hệ thống chữa cháy sprinkler nên không yêu cầu giải pháp ngăn cháy theo phương đứng theo (Đ.4.33.1 đến Đ.4.33.3 Sửa đổi 01:2023 QCVN06/2022-BXD)

MỤC ĐÍCH PHÁT HÀNH / ISSUED FOR

☐	THÔNG TIN / FOR INFORMATION
☐	DỰ TOÁN / FOR ESTIMATE
☒	CHẤP THUẬN / FOR APPROVAL
☐	ĐẤU THẦU / FOR TENDER
☐	ĐIỀU CHỈNH / FOR RESUBMISSION

CHỦ ĐẦU TƯ

HỘ KINH DOANH KARAOKE HOÀNG ANH

TĐS 14, TBĐS 30, PHƯỜNG TÂN PHƯỚC KHÁNH, TP. TÂN UYÊN, TỈNH BÌNH DƯƠNG

ĐƠN VỊ TƯ VẤN THIẾT KẾ XÂY DỰNG

CÔNG TY TNHH ĐẦU TƯ & PHÁT TRIỂN THƯƠNG MẠI DỊCH VỤ KIẾN TRUNG

KIẾN TRUNG

Địa chỉ: Số 310, Quốc lộ 1A, Khu phố 3, Phường Tam Bình, TP. Thủ Đức, TP. Hồ Chí Minh
Điện thoại: 0967 000 485

GIÁM ĐỐC

PHẠM THANH QUANG

CHỦ TRÌ & THIẾT KẾ:

ĐẶNG QUỐC THÁI

THỂ HIỆN:

NGUYỄN PHÚ TOÀN

TÊN DỰ ÁN

CẢI TẠO KARAOKE HOÀNG ANH

TĐS 14, TBĐS 30, PHƯỜNG TÂN PHƯỚC KHÁNH, TP. TÂN UYÊN, TỈNH BÌNH DƯƠNG

TÊN BẢN VẼ

MẶT ĐỨNG CẢI TẠO A-F KARAOKE

HẠNG MỤC

KIẾN TRÚC

KÍ HIỆU.BV	NGÀY HOÀN THÀNH
KT-13	Tháng 12/2024

KÍ HIỆU / SYMBOL:

HƯỚNG THOÁT NẠN

VỊ TRÍ LỐI THOÁT NẠN XA NHẤT

LỐI RA THOÁT NẠN

KÍ HIỆU	GHI CHÚ	GHCL
D1	CỬA KÍNH 1.9 x 2.3m	-
D2	CỬA KÍNH 1.5 x 2.1m	-
FD1	CỬA CHỐNG CHÁY 0.9 x 2.1m	EI60


Ghi chú về cửa chống cháy:
- Các cửa chống cháy D1 GHCL EI60 có cơ cấu tự động đóng kín khi có cháy & đồng thời các khe cửa chống cháy phải được chèn kín

GHSN — Bảng thông báo hạn chế số lượng người trong các phòng karaoke được lắp đặt ngay trên cửa các phòng karaoke


* Ghi chú tính toán bề rộng thoát nạn:
Theo điều G.2.1.1 phụ lục G sửa đổi 01:2023 QCVN 06/2022:
+ Nhà công cộng có bậc chịu lửa II: 165 ng/m
- Tổng chiều rộng lối thoát nạn yêu cầu: $n=\frac{92}{165}=0{,}56m$
- Số lượng lối thoát nạn của karaoke thiết kế: 02 lối bao gồm: 1 lối rộng 1.9 & 1 lối rộng 1.5m

** TÍNH TOÁN KHOẢNG CÁCH THOÁT NẠN:
1, Diện tích đường thoát nạn : S1 = 13.4x1.7+7x4.1+1.4x1.7+4x1.2+2x2.9=64.46M^2
2, Tổng số người của Karaoke là 92 Người
3, Mật độ người của Karaoke là:
MĐ= 92/64.46= 1.43 Người/m^2 < 2 Người/m2
4, Theo bảng G.2a QCVN06:2022/BXD, Công trình có bậc chịu lửa II, MĐ=1.43 ng/m^2<2 ng/m^2.
+ Khoảng cách từ gian phòng đến lối thoát nạn gần nhất từ gian phòng mở ra giữa các lối ra ngoài: 40m
=> Thiết kế vị trí xa nhất, bất lợi nhất cách lối thoát nạn gần nhất là : 13.4m+7m=20.4m<40m (Đảm bảo)

GHI CHÚ:
- Số lượng người có mặt lớn nhất tại Karaoke là 93 người.
- Hành lang thoát nạn có bề rộng = 1.2m, cao > 2.1m.
- Trên đường thoát nạn không bố trí vật dụng, bàn ghế gây cản trở thoát nạn
- Ngăn cháy hành lang thoát nạn:
+ Tường gạch 200mm có GHCL REI150
+ Sàn BTCT có GHCL REI150
+ Trần thạch cao là vật liệu không cháy

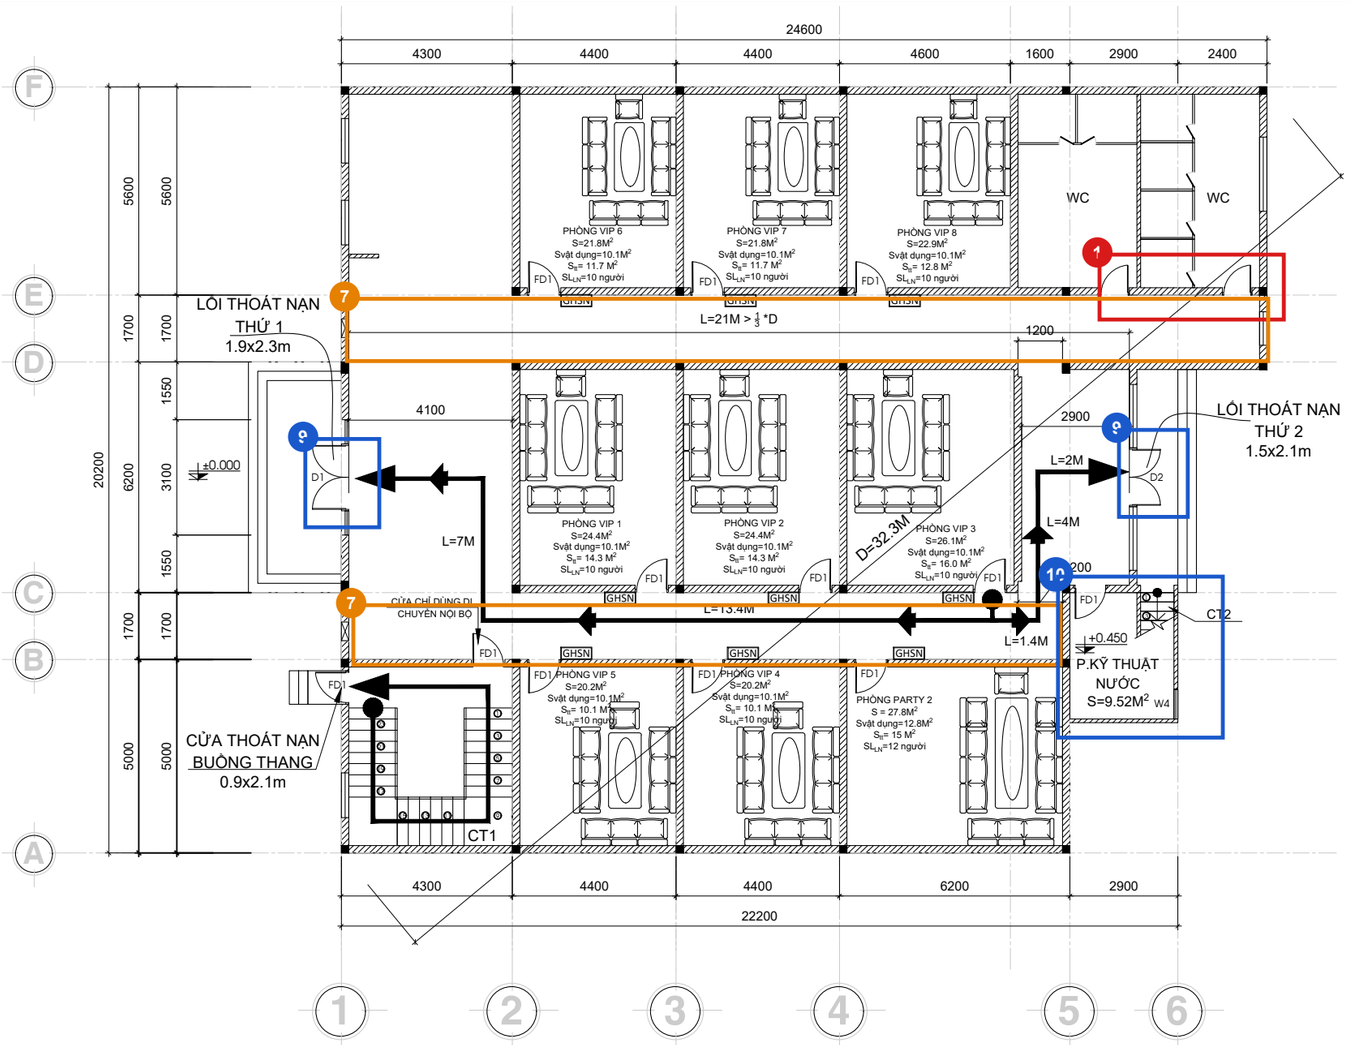

MẶT BẰNG THOÁT NẠN CẢI TẠO TẦNG TRỆT KARAOKE

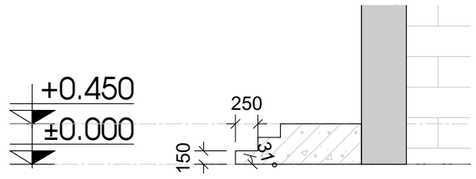

CHI TIẾT BẬC TAM CẤP THOÁT RA NGOÀI NHÀ TRỤC (A-B)/1

GHI CHÚ THẨM ĐỊNH (khung đánh số trên bản vẽ)

1. [CHƯA ĐẠT] D3 (0,8×2,1 m, GHCL '-') mở ra hành lang, không chống cháy (Đ.3.3.5).
2. [CHỈNH BẢN VẼ] Sửa ghi chú: 'cửa chống cháy D1 EI60' thành FD1.
3. [CHỈNH BẢN VẼ] Số người lớn nhất 105 (đã xác nhận): sửa 93 ở bảng thống kê và ghi chú.
5. [CHỈNH BẢN VẼ] Giới hạn 40 m sai so với G.2a (60 m hoặc 30 m); sửa số, kết luận không đổi.
6. [CHỈNH BẢN VẼ] Sửa 'sàn REI150' thành REI45 (đúng thuyết minh kết cấu).
7. [CẦN XÁC NHẬN] Hành lang trong > 15 m không thông gió tự nhiên (D.2c): đã có hút khói, xem khung 14.
8. [CẦN XÁC NHẬN] Thiếu vật liệu tường, sàn hành lang (B.8: CV1 và CV2); cần ghi.
9. [CHỈNH BẢN VẼ] Ghi kích thước bậc tam cấp D1, D2; ghi chú cửa kính hai cánh đẩy mở thủ công, không khóa.
10. [CHỈNH BẢN VẼ] FD1 cạnh P.kỹ thuật nước là cửa phòng dưới thang CT2, không phải lối thoát nạn; nên ghi chú rõ.

*Ghi chú Vật liệu hoàn thiện:
1. Các gian phòng Karaoke được xem là gian phòng chung
2. Các gian phòng Karaoke được trang bị hệ thống chữa cháy tự động Spinkler.
3. Các kết cấu bao che của gian phòng Karaoke là tường gạch dày 200mm GHCL REI150 và cửa gian phòng là cửa chống cháy có GHCL EI60.
=> **Kết luận** : Không yêu cầu về cấp nguy hiểm cháy đối với các vật liệu hoàn thiện, trang trí, ốp lát bên trong gian phòng Karaoke (Theo điều 3.5.10, Sửa đổi 01:2023 QCVN 06:2022 / BXD).

MỤC ĐÍCH PHÁT HÀNH / ISSUED FOR
- ☐ THÔNG TIN / FOR INFORMATION
- ☐ DỰ TOÁN / FOR ESTIMATE
- ☑ CHẤP THUẬN / FOR APPROVAL
- ☐ ĐẤU THẦU / FOR TENDER
- ☐ ĐIỀU CHỈNH / FOR RESUBMISSION

CHỦ ĐẦU TƯ

HỘ KINH DOANH KARAOKE HOÀNG ANH

TĐS 14, TBĐS 30, PHƯỜNG TÂN PHƯỚC KHÁNH, TP. TÂN UYÊN, TỈNH BÌNH DƯƠNG

ĐƠN VỊ TƯ VẤN THIẾT KẾ XÂY DỰNG

CÔNG TY TNHH ĐẦU TƯ & PHÁT TRIỂN THƯƠNG MẠI DỊCH VỤ KIẾN TRUNG

KIẾN TRUNG

Địa chỉ: Số 310, Quốc lộ 1A, Khu phố 3, Phường Tam Bình, TP. Thủ Đức, TP. Hồ Chí Minh
Điện thoại: 0967 000 485

GIÁM ĐỐC

PHẠM THANH QUANG

CHỦ TRÌ & THIẾT KẾ:

ĐẶNG QUỐC THÁI

THỂ HIỆN:

NGUYỄN PHÚ TOÀN

TÊN DỰ ÁN

CẢI TẠO KARAOKE HOÀNG ANH

TĐS 14, TBĐS 30, PHƯỜNG TÂN PHƯỚC KHÁNH, TP. TÂN UYÊN, TỈNH BÌNH DƯƠNG

TÊN BẢN VẼ

MẶT BẰNG THOÁT NẠN CẢI TẠO TẦNG TRỆT KARAOKE

HẠNG MỤC

KIẾN TRÚC

KÍ HIỆU.BV	NGÀY HOÀN THÀNH
KT-16	Tháng 12/2024

KÍ HIỆU / SYMBOL:

HƯỚNG THOÁT NẠN

VỊ TRÍ LỐI THOÁT NẠN XA NHẤT

LỐI RA THOÁT NẠN

KÍ HIỆU	GHI CHÚ	GHCL
D2	CỬA KÍNH 1.5 x 2.1m	-
FD1	CỬA CHỐNG CHÁY 0.9 x 2.1m	EI60

Ghi chú về cửa chống cháy:


- Các cửa chống cháy D1 GHCL EI60 có cơ cấu tự động đóng kín khi có cháy & đồng thời các khe cửa chống cháy phải được chèn kín

GHSN — Bảng thông báo hạn chế số lượng người trong các phòng karaoke được lắp đặt ngay trên cửa các phòng karaoke

* Ghi chú tính toán bề rộng thoát nạn:
Theo điều G.2.1.1 phụ lục G sửa đổi 01:2023 QCVN 06/2022:
+ Nhà công cộng có bậc chịu lửa II: 165 ng/m
- Tổng chiều rộng lối thoát nạn yêu cầu: $n=\frac{105}{165}=0,64m$
- Số lượng lối thoát nạn của karaoke thiết kế: 02 lối bao gồm: 1 lối rộng 0.9 & 1 lối rộng 0.9m

** TÍNH TOÁN KHOẢNG CÁCH THOÁT NẠN:
1, Diện tích đường thoát nạn : S1 = 13.1x1.7+8.4x1.9+4.5x1.7+1.5x1.2+4.3x2.9=60.15M^2
2, Tổng số người của Karaoke là 105 Ngườ
3, Mật độ người của Karaoke là:
MĐ= 105/60.15= 1.75 Người/m^2 < 2 Người/m2
4, Theo bảng G.2a QCVN06:2022/BXD, Công trình có bậc chịu lửa II, MĐ=1.75 ng/m^2<2 ng/m^2.
+ Khoảng cách từ gian phòng đến lối thoát nạn gần nhất từ gian phòng mở ra giữa các lối ra ngoài: 40m
=> Thiết kế vị trí xa nhất, bất lợi nhất cách lối thoát nạn gần nhất là : 13.1m+8.4m=21.5m<40m (Đảm bảo)

GHI CHÚ:
- Số lượng người có mặt lớn nhất tại Karaoke là 105 người.
- Hành lang thoát nạn có bề rộng = 1.2m, cao > 2.1m.
- Trên đường thoát nạn không bố trí vật dụng, bàn ghế gây cản trở thoát nạn
- Ngăn cháy hành lang thoát nạn:
+ Tường gạch 200mm có GHCL REI150
+ Sàn BTCT có GHCL REI150
+ Trần thạch cao là vật liệu không cháy

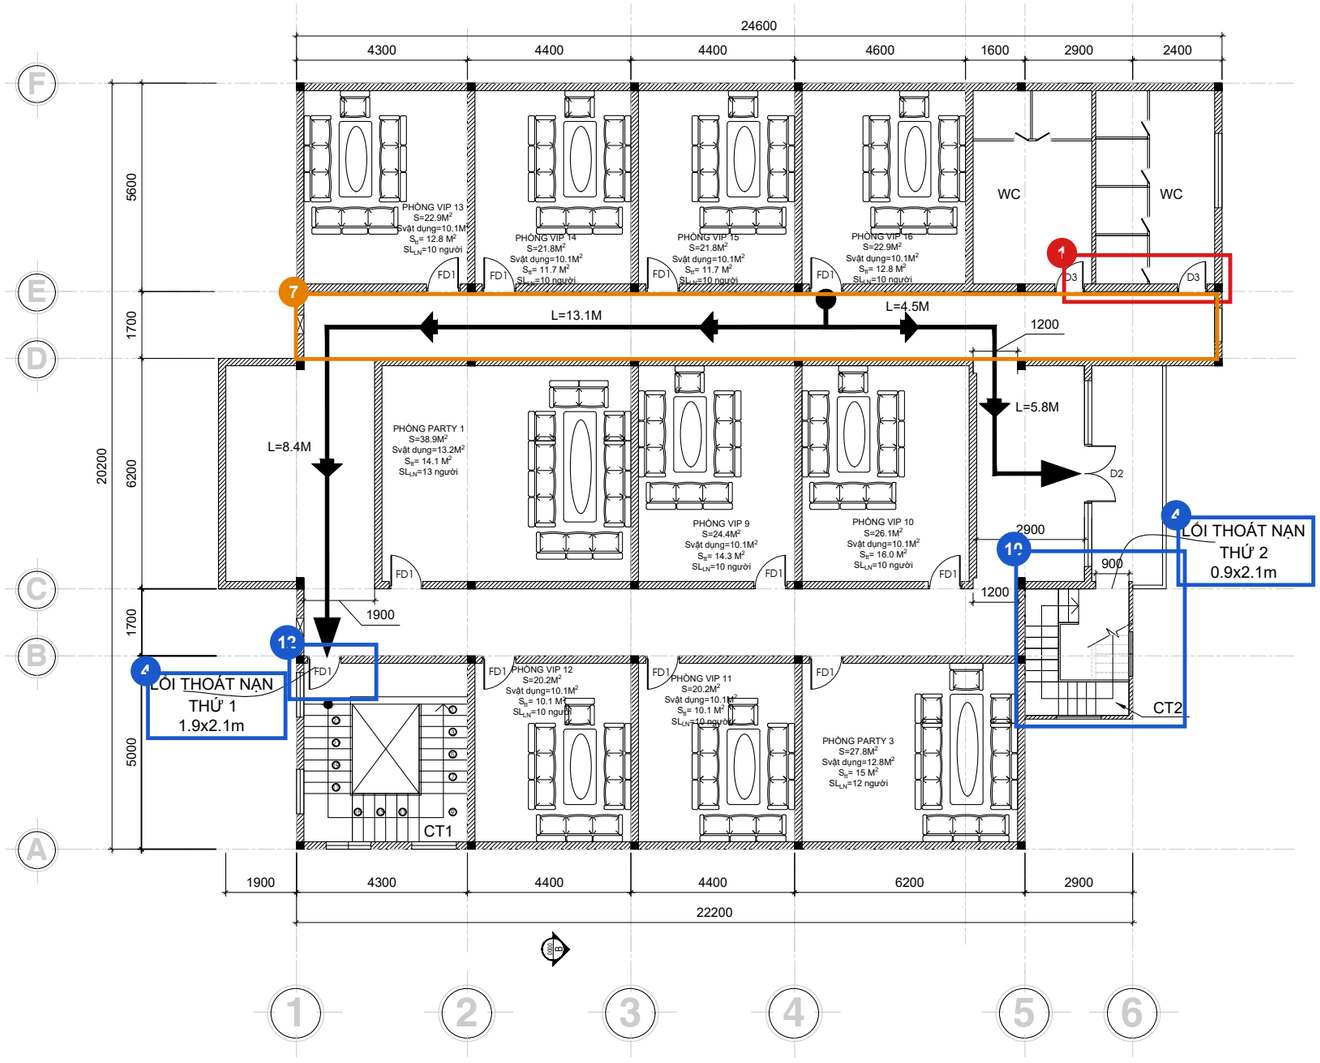

MẶT BẰNG THOÁT NẠN CẢI TẠO LẦU 1 KARAOKE

GHI CHÚ THẨM ĐỊNH (khung đánh số trên bản vẽ)

1. [CHƯA ĐẠT] D3 (0,8×2,1 m, GHCL '-') mở ra hành lang, không chống cháy (Đ.3.3.5).
2. [CHỈNH BẢN VẼ] Sửa ghi chú: 'cửa chống cháy D1 EI60' thành FD1.
3. [CHỈNH BẢN VẼ] Số người lớn nhất 105 (đã xác nhận): sửa 93 ở bảng thống kê và ghi chú.
4. [CHỈNH BẢN VẼ] Lầu 1: sửa nhãn lối 1 là FD1 0,9 m, lối 2 là D2 1,5 m; sửa ghi chú tổng.
5. [CHỈNH BẢN VẼ] Giới hạn 40 m sai so với G.2a (60 m hoặc 30 m); sửa số, kết luận không đổi.
6. [CHỈNH BẢN VẼ] Sửa 'sàn REI150' thành REI45 (đúng thuyết minh kết cấu).
7. [CẦN XÁC NHẬN] Hành lang trong > 15 m không thông gió tự nhiên (D.2c): đã có hút khói, xem khung 14.
10. [CHỈNH BẢN VẼ] FD1 cạnh P.kỹ thuật nước là cửa phòng dưới thang CT2, không phải lối thoát nạn; nên ghi chú rõ.
12. [CHỈNH BẢN VẼ] Bổ sung kiểm tra từng lối khi một lối bị chặn: 105 người qua FD1 0,9 m (0,9×165 = 148, đạt).

*Ghi chú Vật liệu hoàn thiện:
1. Các gian phòng Karaoke được xem là gian phòng chung
2. Các gian phòng Karaoke được trang bị hệ thống chữa cháy tự động Spinkler.
3. Các kết cấu bao che của gian phòng Karaoke là tường gạch dày 200mm GHCL REI150 và cửa gian phòng là cửa chống cháy có GHCL EI60.
=> **Kết luận** : Không yêu cầu về cấp nguy hiểm cháy đối với các vật liệu hoàn thiện, trang trí, ốp lát bên trong gian phòng Karaoke (Theo điều 3.5.10, Sửa đổi 01:2023 QCVN 06:2022 / BXD).

MỤC ĐÍCH PHÁT HÀNH / ISSUED FOR

- ☐ THÔNG TIN / FOR INFORMATION
- ☐ DỰ TOÁN / FOR ESTIMATE
- ☑ CHẤP THUẬN / FOR APPROVAL
- ☐ ĐẤU THẦU / FOR TENDER
- ☐ ĐIỀU CHỈNH / FOR RESUBMISSION

CHỦ ĐẦU TƯ

HỘ KINH DOANH KARAOKE HOÀNG ANH
TĐS 14, TBĐS 30, PHƯỜNG TÂN PHƯỚC KHÁNH, TP. TÂN UYÊN, TỈNH BÌNH DƯƠNG

ĐƠN VỊ TƯ VẤN THIẾT KẾ XÂY DỰNG

CÔNG TY TNHH ĐẦU TƯ & PHÁT TRIỂN THƯƠNG MẠI DỊCH VỤ KIẾN TRUNG
KIẾN TRUNG
Địa chỉ: Số 310, Quốc lộ 1A, Khu phố 3, Phường Tam Bình, TP. Thủ Đức, TP. Hồ Chí Minh
Điện thoại: 0967 000 485

GIÁM ĐỐC
PHẠM THANH QUANG

CHỦ TRÌ & THIẾT KẾ:
ĐẶNG QUỐC THÁI

THỂ HIỆN:
NGUYỄN PHÚ TOÀN

TÊN DỰ ÁN
CẢI TẠO KARAOKE HOÀNG ANH
TĐS 14, TBĐS 30, PHƯỜNG TÂN PHƯỚC KHÁNH, TP. TÂN UYÊN, TỈNH BÌNH DƯƠNG


TÊN BẢN VẼ
MẶT BẰNG THOÁT NẠN CẢI TẠO LẦU 1 KARAOKE

HẠNG MỤC
KIẾN TRÚC


KÍ HIỆU.BV	NGÀY HOÀN THÀNH
KT-17	Tháng 12/2024

***Ghi chú ngăn cháy hành lang thoát nạn:
* Các hành lang thoát nạn được bảo vệ bởi tường gạch 200mm GHCL REI150 & cửa chống cháy GHCL EI60 (Đảm bảo Đ.3.3.5 sửa đổi 01:2023 QCVN06/2022-BXD)
* Tổng chiều dài hành lang thoát nạn:
L=L1+L2=13.4+7=20.4m
=> Không yêu cầu giải pháp ngăn cháy hành lang thoát nạn (Đảm bảo Đ.3.3.5 sửa đổi 01:2023 QCVN06/2022-BXD)

KÍ HIỆU	GHI CHÚ	GHCL
D1	CỬA KÍNH 1.9 x 2.3m	-
D2	CỬA KÍNH 1.5 x 2.1m	-
D3	CỬA 0.8 x 2.1m	-
D4	CỬA WC 0.8 x 1.9m	-
FD1	CỬA CHỐNG CHÁY 0.9 x 2.1m	EI60
W1	CỬA SỔ 1 x 1.4m	-
W2	Ô KÍNH LẤY SÁNG 1 x 1.4m	-
W3	CỬA SỔ 0.9 x 1m	-
W4	Ô KÍNH LẤY SÁNG 0.8 x 1.5m	-
W5	Ô KÍNH LẤY SÁNG 2 x 0.3m	-
W6	Ô KÍNH LẤY SÁNG 0.8x1.5	-

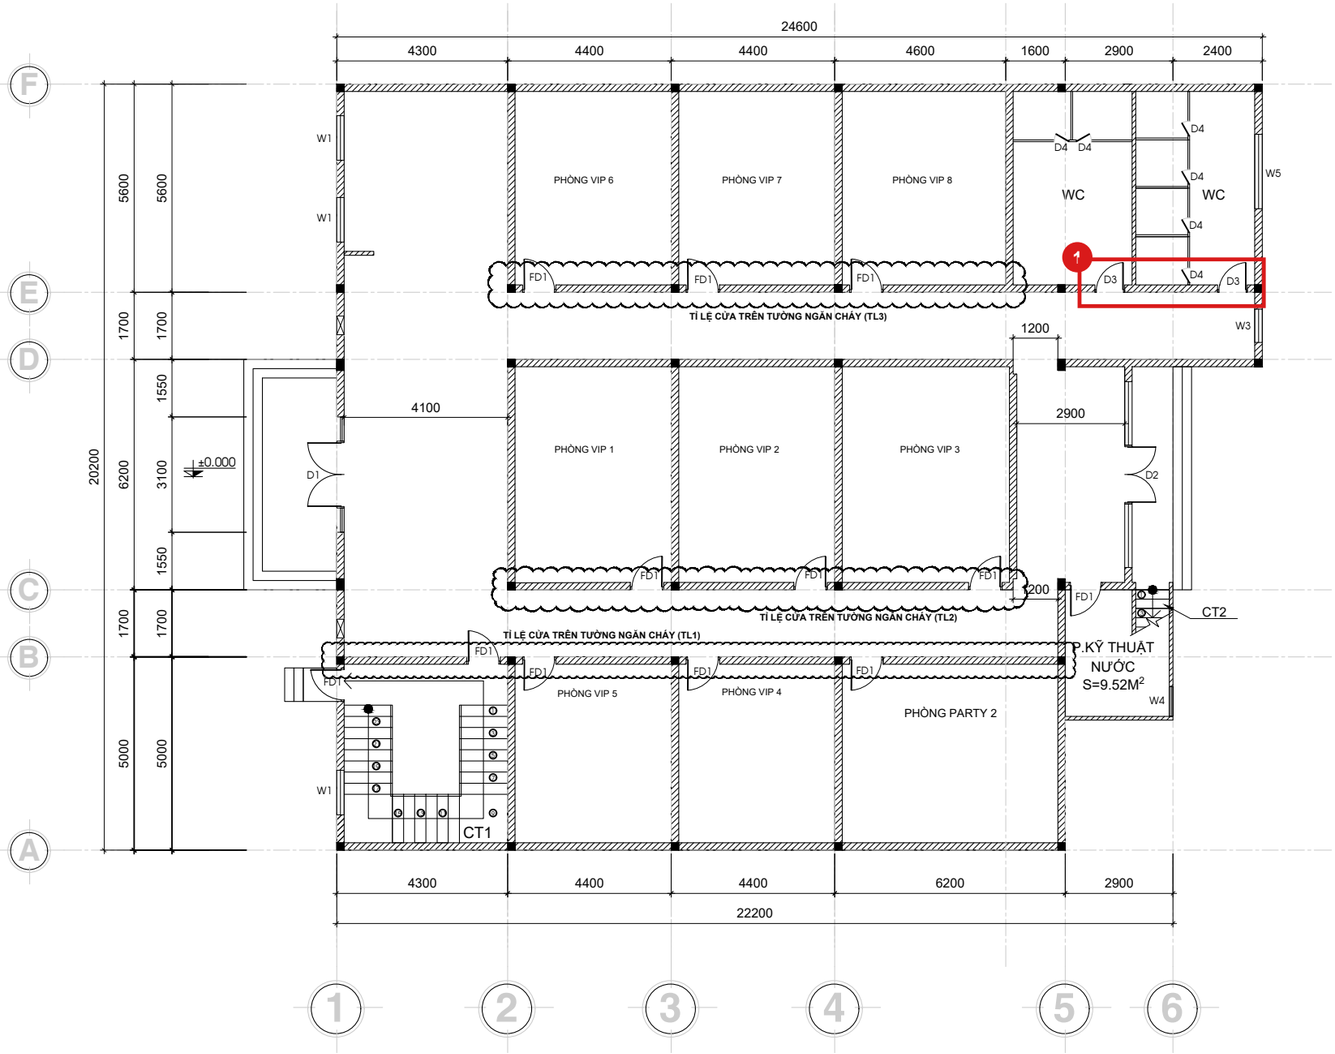

MẶT BẰNG NGĂN CHÁY CẢI TẠO TẦNG TRỆT KARAOKE

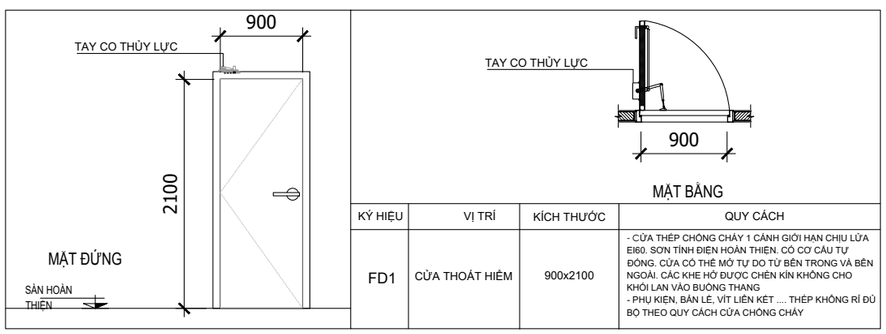

KÝ HIỆU	VỊ TRÍ	KÍCH THƯỚC	QUY CÁCH
FD1	CỬA THOÁT HIỂM	900x2100	- CỬA THÉP CHỐNG CHÁY 1 CÁNH GIỚI HẠN CHỊU LỬA EI60. SƠN TĨNH ĐIỆN HOÀN THIỆN. CÓ CƠ CẤU TỰ ĐÓNG. CỬA CÓ THỂ MỞ TỰ DO TỪ BÊN TRONG VÀ BÊN NGOÀI. CÁC KHE HỞ ĐƯỢC CHÈN KÍN KHÔNG CHO KHÓI LAN VÀO BUỒNG THANG - PHỤ KIỆN, BẢN LỀ, VÍT LIÊN KẾT .... THÉP KHÔNG RỈ ĐỦ BỘ THEO QUY CÁCH CỬA CHỐNG CHÁY

CHI TIẾT CỬA CHỐNG CHÁY-FD1

GHI CHÚ THẨM ĐỊNH (khung đánh số trên bản vẽ)

1. [CHƯA ĐẠT] D3 (0,8×2,1 m, GHCL '-') mở ra hành lang, không chống cháy (Đ.3.3.5).

2. [CHỈNH BẢN VẼ] Sửa ghi chú: 'cửa chống cháy D1 EI60' thành FD1.

11. [CẦN XÁC NHẬN] Bảng tỉ lệ cửa/tường chỉ tính FD1; TL3 còn cửa D3 không chống cháy.

Ghi chú về cửa chống cháy:
2
- Các cửa chống cháy D1 GHCL EI60 có cơ cấu tự động đóng kín khi có cháy & đồng thời các khe cửa chống cháy phải được chèn kín

HẠNG MỤC	CHIỀU CAO TƯỜNG (M)	CHIỀU DÀI TƯỜNG (M)	TỔNG DT TƯỜNG NGĂN CHÁY-S1 (M2)	KT CỬA CHỐNG CHÁY (M)	SỐ LƯỢNG CỬA CHỐNG CHÁY	TỔNG DT CỬA CHỐNG CHÁY-S2 (M2)	TỈ LỆ S1/S2(%)	KẾT LUẬN (<25%)
TƯỜNG TL1	4	19.2	76.8	0,9X2,1=1,89	4	7.56	9.84	ĐẢM BẢO
TƯỜNG TL2	4	13.7	54.8		3	5.67	10.35	ĐẢM BẢO
TƯỜNG TL3	4	13.7	54.8		3	5.67	10.35	ĐẢM BẢO

11

MỤC ĐÍCH PHÁT HÀNH / ISSUED FOR
- ☐ THÔNG TIN / FOR INFORMATION
- ☐ DỰ TOÁN / FOR ESTIMATE
- ☑ CHẤP THUẬN / FOR APPROVAL
- ☐ ĐẤU THẦU / FOR TENDER
- ☐ ĐIỀU CHỈNH / FOR RESUBMISSION

CHỦ ĐẦU TƯ

HỘ KINH DOANH KARAOKE HOÀNG ANH

TĐS 14, TBĐS 30, PHƯỜNG TÂN PHƯỚC KHÁNH, TP. TÂN UYÊN, TỈNH BÌNH DƯƠNG

ĐƠN VỊ TƯ VẤN THIẾT KẾ XÂY DỰNG

CÔNG TY TNHH ĐẦU TƯ & PHÁT TRIỂN THƯƠNG MẠI DỊCH VỤ KIẾN TRUNG

KIẾN TRUNG

Địa chỉ: Số 310, Quốc lộ 1A, Khu phố 3, Phường Tam Bình, TP. Thủ Đức, TP. Hồ Chí Minh
Điện thoại: 0967 000 485

GIÁM ĐỐC

PHẠM THANH QUANG

CHỦ TRÌ & THIẾT KẾ:

ĐẶNG QUỐC THÁI

THỂ HIỆN:

NGUYỄN PHÚ TOÀN

TÊN DỰ ÁN

CẢI TẠO KARAOKE HOÀNG ANH

TĐS 14, TBĐS 30, PHƯỜNG TÂN PHƯỚC KHÁNH, TP. TÂN UYÊN, TỈNH BÌNH DƯƠNG

TÊN BẢN VẼ

MẶT BẰNG NGĂN CHÁY CẢI TẠO TẦNG TRỆT KARAOKE

HẠNG MỤC


KIẾN TRÚC

KÍ HIỆU.BV	NGÀY HOÀN THÀNH
KT-18	Tháng 12/2024


Ghi chú về cửa chống cháy:
- Các cửa chống cháy D1 GHCL EI60 có cơ cấu tự động đóng kín khi có cháy & đồng thời các khe cửa chống cháy phải được chèn kín

***Ghi chú ngăn cháy hành lang thoát nạn:
* Các hành lang thoát nạn được bảo vệ bởi tường gạch 200mm GHCL REI150 & cửa chống cháy GHCL EI60 (Đảm bảo Đ.3.3.5 sửa đổi 01:2023 QCVN06/2022-BXD)
* Tổng chiều dài hành lang thoát nạn:
L=L1+L2=13.1+8.4=21.5m
=> Không yêu cầu giải pháp ngăn cháy hành lang thoát nạn (Đảm bảo Đ.3.3.5 sửa đổi 01:2023 QCVN06/2022-BXD)

KÍ HIỆU	GHI CHÚ	GHCL
D2	CỬA KÍNH 1.5 x 2.1m	-
D3	CỬA 0.8 x 2.1m	-
D4	CỬA WC 0.8 x 1.9m	-
FD1	CỬA CHỐNG CHÁY 0.9 x 2.1m	EI60
W1	CỬA SỔ 1 x 1.4m	-
W2	Ô KÍNH LẤY SÁNG 1x1.4m	-
W3	CỬA SỔ 0.9 x 1m	-
W5	Ô CỬA LẤY SÁNG 2 x 0.3m	-

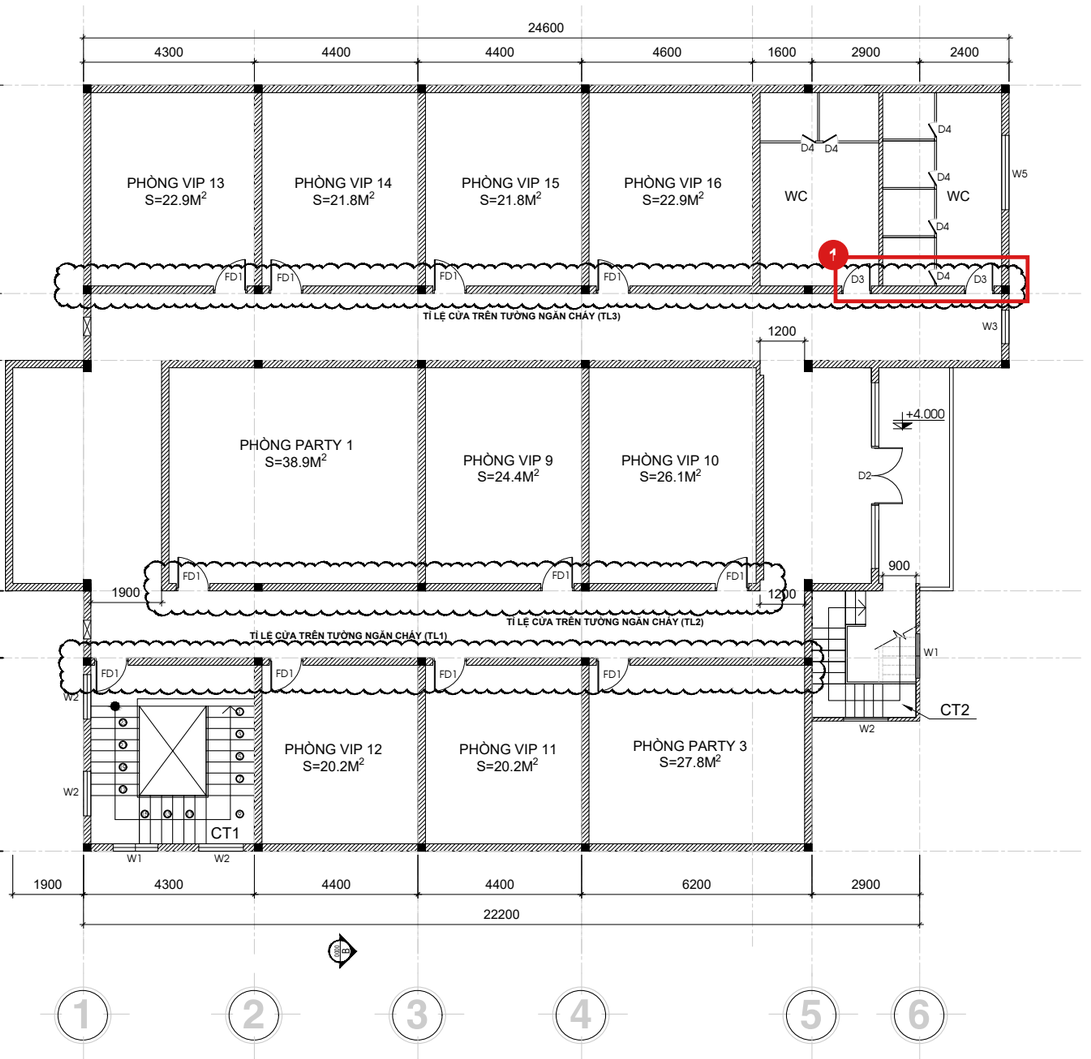

MẶT BẰNG THOÁT NẠN CẢI TẠO LẦU 1 KARAOKE

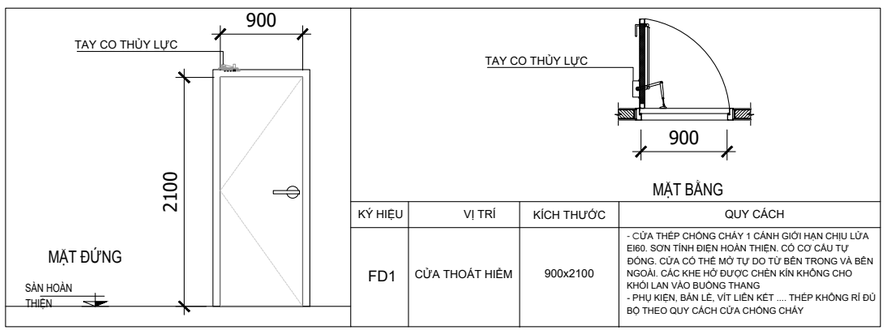

KÝ HIỆU	VỊ TRÍ	KÍCH THƯỚC	QUY CÁCH
FD1	CỬA THOÁT HIỂM	900x2100	- CỬA THÉP CHỐNG CHÁY 1 CÁNH GIỚI HẠN CHỊU LỬA EI60. SƠN TĨNH ĐIỆN HOÀN THIỆN. CÓ CƠ CẤU TỰ ĐÓNG. CỬA CÓ THỂ MỞ TỰ DO TỪ BÊN TRONG VÀ BÊN NGOÀI. CÁC KHE HỞ ĐƯỢC CHÈN KÍN KHÔNG CHO KHÓI LAN VÀO BUỒNG THANG - PHỤ KIỆN, BẢN LỀ, VÍT LIÊN KẾT .... THÉP KHÔNG RỈ ĐỦ BỘ THEO QUY CÁCH CỬA CHỐNG CHÁY

CHI TIẾT CỬA CHỐNG CHÁY-FD1

GHI CHÚ THẨM ĐỊNH (khung đánh số trên bản vẽ)
1. [CHƯA ĐẠT] D3 (0,8×2,1 m, GHCL '-') mở ra hành lang, không chống cháy (Đ.3.3.5).
2. [CHỈNH BẢN VẼ] Sửa ghi chú: 'cửa chống cháy D1 EI60' thành FD1.
11. [CẦN XÁC NHẬN] Bảng tỉ lệ cửa/tường chỉ tính FD1; TL3 còn cửa D3 không chống cháy.

HẠNG MỤC	CHIỀU CAO TƯỜNG (M)	CHIỀU DÀI TƯỜNG (M)	TỔNG DT TƯỜNG NGĂN CHÁY-S1 (M2)	KT CỬA CHỐNG CHÁY (M)	SỐ LƯỢNG CỬA CHỐNG CHÁY	TỔNG DT CỬA CHỐNG CHÁY-S2 (M2)	TỈ LỆ S1/S2(%)	KẾT LUẬN (<25%)
TƯỜNG TL1	3.6	19.2	69.12	0,9X2,1=1,89	4	7.56	10.94	ĐẢM BẢO
TƯỜNG TL2	3.6	16.2	58.32		3	5.67	9.72	ĐẢM BẢO
TƯỜNG TL3	3.6	24.5	88.2		4	7.56	8.57	ĐẢM BẢO

MỤC ĐÍCH PHÁT HÀNH / ISSUED FOR
- ☐ THÔNG TIN / FOR INFORMATION
- ☐ DỰ TOÁN / FOR ESTIMATE
- ☑ CHẤP THUẬN / FOR APPROVAL
- ☐ ĐẤU THẦU / FOR TENDER
- ☐ ĐIỀU CHỈNH / FOR RESUBMISSION

CHỦ ĐẦU TƯ

HỘ KINH DOANH KARAOKE HOÀNG ANH
TĐS 14, TBĐS 30, PHƯỜNG TÂN PHƯỚC KHÁNH, TP. TÂN UYÊN, TỈNH BÌNH DƯƠNG

ĐƠN VỊ TƯ VẤN THIẾT KẾ XÂY DỰNG

CÔNG TY TNHH ĐẦU TƯ & PHÁT TRIỂN THƯƠNG MẠI DỊCH VỤ KIẾN TRUNG
KIẾN TRUNG
Địa chỉ: Số 310, Quốc lộ 1A, Khu phố 3, Phường Tam Bình, TP. Thủ Đức, TP. Hồ Chí Minh
Điện thoại: 0967 000 485

GIÁM ĐỐC
PHẠM THANH QUANG

CHỦ TRÌ & THIẾT KẾ:
ĐẶNG QUỐC THÁI

THỂ HIỆN:
NGUYỄN PHÚ TOÀN

TÊN DỰ ÁN
CẢI TẠO KARAOKE HOÀNG ANH
TĐS 14, TBĐS 30, PHƯỜNG TÂN PHƯỚC KHÁNH, TP. TÂN UYÊN, TỈNH BÌNH DƯƠNG

TÊN BẢN VẼ
MẶT BẰNG THOÁT NẠN CẢI TẠO LẦU 1 KARAOKE

HẠNG MỤC
KIẾN TRÚC

KÍ HIỆU.BV	NGÀY HOÀN THÀNH
KT-19	Tháng 12/2024

THUYẾT MINH:

* **Tiêu chuẩn áp dụng:**

- Sửa đổi 01:2023 QCVN 06:2022/BXD & QCVN 06:2022/BXD: Quy chuẩn kỹ thuật quốc gia về an toàn cháy cho nhà và công trình.
- TCVN 3890:2023: Phương tiện phòng cháy và chữa cháy cho nhà và công trình - Trang bị, bố trí, kiểm tra, bảo dưỡng.
- TCVN 13456:2022 Phòng cháy chữa cháy – Phương tiện chiếu sáng sự cố và chỉ dẫn thoát nạn – Yêu cầu thiết kế, lắp đặt.

* **Quy định chung:**

+ Việc thiết kế, lắp đặt phương tiện chiếu sáng và chỉ dẫn thoát nạn phải tuân thủ các yêu cầu, quy định của các quy chuẩn, tiêu chuẩn, quy phạm hiện hành.

+ Đèn chiếu sáng sự cố và biển báo an toàn có nguồn điện dự phòng phải đảm bảo thời gian hoạt động ổn định liên tục tối thiểu 120 phút khi có sự cố cháy, nổ

+ Biển báo an toàn phải được nhìn thấy rõ ràng các chứ "LỐI RA" hoặc chữ "EXIT", ký hiệu hình hóc khác thích hợp. Màu sắc của biển báo an toàn: màu nền là màu xanh lá cây, màu chữ và ký hiệu hình học là màu trắng.

+ Phương tiện chiếu sáng sự cố và chỉ dẫn thoát nạn phải được lựa chọn, trang bị phù hợp để đảm bảo tầm nhìn thoát nạn, chỉ thị rõ ràng đường thoát nạn, cảnh báo những vị trí có nguy cơ gây nguy hiểm trong quá trình thoát nạn và nhận biết các vị trí trang bị các thiết bị phòng cháy và chữa cháy.

* **Thuyết minh lắp đặt:**

Lắp đặt đèn chiếu sáng sự cố và biển báo an toàn phải phù hợp theo quy định của TCVN 7722-2-22:2013. Khi lắp đặt đèn chiếu sáng sự cố và biển báo an toàn trong nhà, công trình, hạng mục công trình có nguy hiểm về nổ hoặc độ ẩm cao phải sử dụng các đèn, biển báo có khả năng chống nổ hoặc chống ẩm

- **Phương tiện chiếu sáng sự cố:**

+ Đối với chiếu sáng sự cố đường thoát nạn: có chiều rộng đến 2m, thì độ rọi trung bình theo phương nằm ngang trên mặt sàn dọc theo tâm của đường thoát nạn phải lớn hơn hoặc bằng 1 lux và ở dải giữa với chiều rộng lớn hơn hoặc bằng một nửa chiều rộng của đường thoát nạn phải được chiếu sáng tối thiểu 50% giá trị đó.

+ Đối với chiếu sáng sự cố gian phòng: Độ rọi trung bình theo phương nằm ngang không được nhỏ hơn 0.5 lux tại mặt sàn tại mọi điểm lõi của khoảng trống, không bao gồm đường viền 0.5m theo chu vi khu vực.

+ Tỉ lệ giữa độ rọi lớn nhất và độ rọi nhỏ nhất dọc theo đường tâm của đường thoát nạn và chiếu sáng khoảng trống (chống hoảng loạn) không được lớn hơn 40:1

+ Phải đảm bảo giảm thiểu nguy cơ gây lóa tạm thời bằng cách hạn chế cường độ sáng ở giai đoạn phát sáng cực đại trong chế độ hoạt động khi có sự cố của mỗi đèn thuộc phạm vi quan sát. Cụ thể:

. Đối với việc chiếu sáng đường thoát nạn theo phương ngang so với mặt sàn,chiếu sáng gian phòng và chiếu sáng các phương tiện phòng cháy và chữa cháy, cường độ chiếu sáng của các đèn trong phạm vi góc chiếu từ 60° đến 90° không được vượt quá giá trị quy định tại Bảng 1.

. Đối với đường thoát nạn khác, cường độ chiếu sáng của các đèn không được vượt quá giá trị tại Bảng 1 ở bất kỳ góc chiếu nào.

+ Các tủ trung tâm báo cháy, nút nhấn báo cháy và phương tiện chữa cháy phải được chiếu sáng đầy đủ để có thể dễ dàng xác định vị trí và nếu không nằm trên đường thoát nạn hoặc không nằm trong một phạm vi khoảng trống thì phải được chiếu sáng tối thiểu 5 Lux tại mặt sàn.

- **Chỉ dẫn thoát nạn:**

+ Biển báo chỉ dẫn lối thoát nạn ở tất cả các lối dẫn tới đường thoát nạn. Trường hợp biển chỉ dẫn thoát nạn bị che khuất tầm nhìn cần trang bị bổ sung biển chỉ hướng.

+ Vị trí lắp đặt giữa các biển báo an toàn (không bao gồm biển báo an toàn tầm thấp) phải đảm bảo khoảng cách không lớn hơn 25m. Biển báo an toàn (không bao gồm biển báo an toàn tầm thấp) phải lắp đặt ở độ cao từ 2-2.7m so với sàn hoàn thiện hoặc ngay trên đầu cửa có chiều cao lớn hơn 2.7m. Các khu vực không được bảo vệ chống khói khiến khói tích tụ thì biển báo an toàn nên được gắn thấp hơn trần nhà tối thiểu 0.5m. Không được lắp biển báo an toàn được chiếu sáng từ bên ngoài

Tại các tầng có diện tích lớn hơn 1000m2 hoặc có từ 2 lối thoát nạn trở lên phải có sơ đồ chỉ dẫn thoát nạn.Nằm tại độ cao 1.5±0.2m so với mặt sàn hoàn thiện.

+ Sơ đồ chỉ dẫn thoát nạn gồm 2 phần: phần bằng chữ và phần ký hiệu hình học. Sơ đồ chỉ dẫn thoát nạn phải được niêm yết tại vị trí dễ nhận biết, dễ thấy và vị trí có người thường xuyên qua lại.

+ Phần ký hiệu hình học bao gồm mặt bằng tầng, lối ra chỉ hướng thoát nạn, cầu thang bộ, vị trí sơ đồ tại tầng , vị trí đặt phương tiện, thiết bị chữa cháy và cứu nạn, cứu hộ.

+ Phần chỉ dẫn bằng chứ gồm nội dung và trình tự xử lý khi có cháy.

Kích thước của sơ đồ chỉ dẫn thoát nạn phụ thuộc vào đặc tính, tính chất hoạt động, diện tích của tầng, phòng; phương án thoát nạn nhưng không được nhỏ hơn:

600x400 mm - đối với sơ đồ chỉ dẫn tại tầng;

400x300 mm - đối với sơ đồ chỉ dẫn tại phòng.

- Tính toán độ rọi cho đường thoát nạn tầng 1 (theo phương pháp chung đều): E=ksd*Φ/S

Trong đó:

Φ: tổng quang thông của 10 bộ đèn thoát nạn 10w =10*10*100=10.000 (lm)

15 S: là tổng diện tích lối thoát nạn = 1601,7m2

Ksd: Chọn hệ số sử dụng là 0,4 QTTSP < Q tối thiểu

+ Vậy:

15 E=0,4*10.000/820 = 12, 19 (lux)

- Tính toán chiều cao nhỏ nhất cho phép của biển báo an toàn: H= L/Z

Trong đó:

H : chiều cao nhỏ nhất cho phép của biển báo an toàn

15 L : khoảng cách quan sát (m), căn cứ bản vẽ chọn khoảng cách bất lợi nhất là 85m

15 Z: hằng số, trong đó Z=200 áp dụng cho các biển báo nhìn từ bên trong

Vậy: H=L/Z=30/200=0.15m.

Thiết kế chọn đèn biển báo thoát nạn có chiều cao là 202, chiều dài là 370.

- Tính toán độ chói lóa :

L= Φ/Φ/Steradian

Trong đó:

L: Độ chói lóa của đèn

Φ: quang thông của 1 bộ đèn thoát nạn 10w

=10*100=1.000 (lm) Steradian: đèn lắp trên tường có góc steradian là 1/2 hình cầu, vậy

Steradian = 2Π

+ Vậy:

L = 1000/(2Π) = 159cd

Căn cứ điều 5.1 TCVN 13456:2022 bảng 1, lắp đặt đèn chi

cao độ 2.6m có độ chói lóa cho phép là 900cd. Vậy phươn

sáng sự cố phù hợp TCVN 13456:2022

Tại các vị trí bình chữa cháy + tủ chữa cháy bằng nước + nút nhấn, bố trí đèn chiếu sáng sự cố trực tiếp tại các vị trí này có độ rọi trung bình như tính toán ở trên, cụ thể là 13 lux . Đèn chỉ dẫn thoát nạn

GHI CHÚ THẨM ĐỊNH (khung đánh số trên bản vẽ)

15. [CHỈNH BẢN VẼ] EX–EM: E = 4,88 lux (ghi 12,19); S ghi 1 601,7 tính 820; L ghi 85 m tính 30 m. Sửa số.

MỤC ĐÍCH PHÁT HÀNH / ISSUED FOR

- ☐ THÔNG TIN / FOR INFORMATION
- ☐ DỰ TOÁN / FOR ESTIMATE
- ☑ CHẤP THUẬN / FOR APPROVAL
- ☐ ĐẤU THẦU / FOR TENDER
- ☐ ĐIỀU CHỈNH / FOR RESUBMISSION

CHỦ ĐẦU TƯ

HỘ KINH DOANH KARAOKE HOÀNG ANH

ĐƠN VỊ TƯ VẤN THIẾT KẾ

CÔNG TY TNHH MTV HOÀNG QUÂN PHÁT

Địa chỉ: 521/14 Kp. Tân Hòa, P. Đông Hòa, TP. Dĩ An, T. Bình Dương
Điện thoại: 0986 099 519 - 028 6656 6422
Email: hoangquanphat@gmail.com
website: http://pccc24.com

GIÁM ĐỐC

LÊ BÍCH TRANG

CHỦ TRÌ & THIẾT KẾ:

VŨ QUYẾT TIẾN

THỂ HIỆN:

TRẦN TRỌNG TIẾN

TÊN DỰ ÁN

CẢI TẠO KARAOKE HOÀNG ANH

Địa chỉ: KP. Bình Hòa 2, P. Tân Phước Khánh, TP. Tân Uyên, Tỉnh Bình Dương


TÊN BẢN VẼ

THUYẾT MINH HỆ THỐNG ĐÈN EX - EM

HẠNG MỤC

ĐÈN EX - EM

KÍ HIỆU.BV	NGÀY HOÀN THÀNH
EXEM-05	Tháng 10/2024

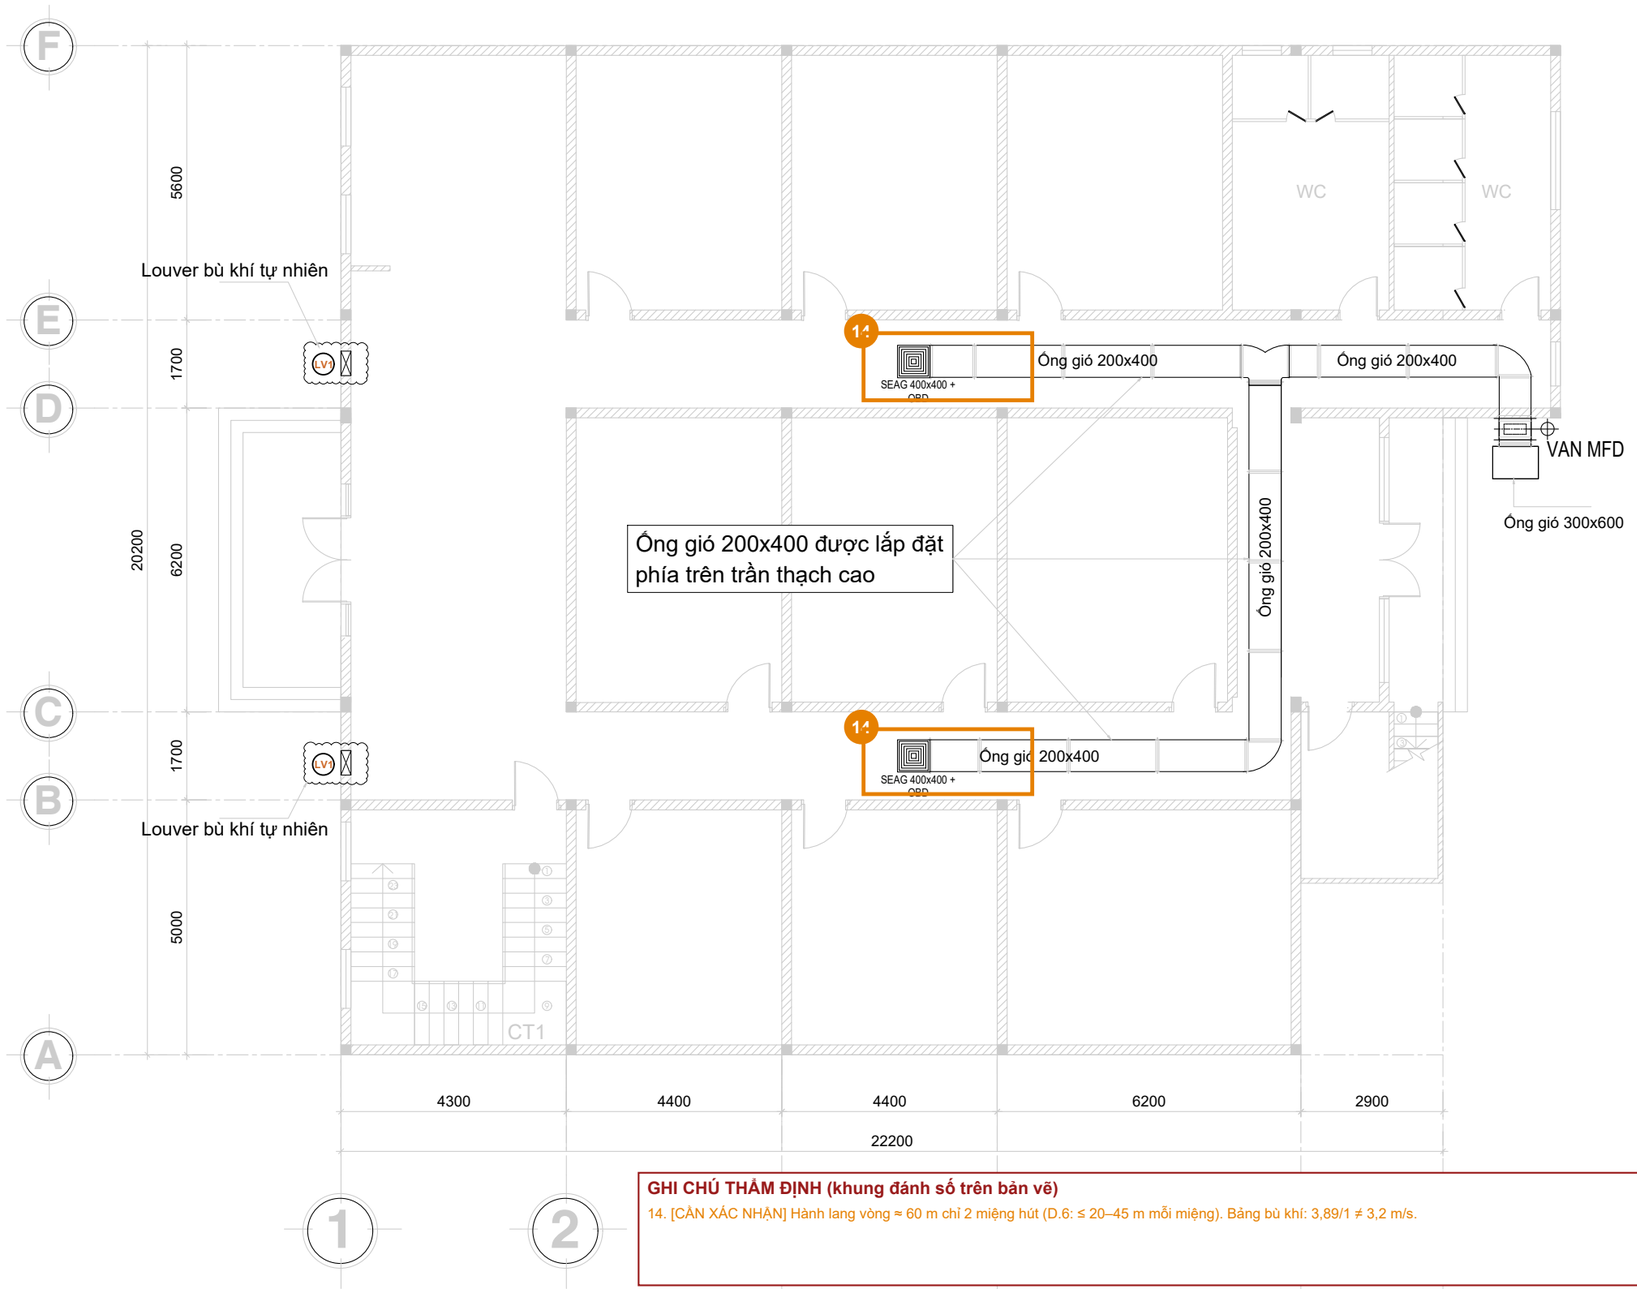

GHI CHÚ THẨM ĐỊNH (khung đánh số trên bản vẽ)


14. [CẦN XÁC NHẬN] Hành lang vòng ≈ 60 m chỉ 2 miệng hút (D.6: ≤ 20–45 m mỗi miệng). Bảng bù khí: 3,89/1 ≠ 3,2 m/s.

MẶT BẰNG HÚT KHÓI TẦNG TRỆT

1) Ống gió được làm bằng thép mạ kẽm có chiều dày tối thiểu 1,2 mm.
2) toàn bộ chiều dài ống được bảo vệ bằng các đầu phun sprinkler và các đầu phun được bố trí bên trên và bên dưới ống.
3) ống và kết cấu treo, đỡ được thiết kế và thi công phù hợp với quy cách hiện hành.
=> Không yêu cầu GHCL của ống gió hút khói (chú thích 4, mục D.9 phụ lục D sửa đổi 01:2023 QCVN 06/2022-BXD).

CHỮ VIẾT TẮT/KÝ HIỆU			
SEAG	MIỆNG HÚT KHÓI	MFD	CỬA GIÓ ĐÓNG MỞ BẰNG ĐỘNG CƠ ĐIỆN
OBD	CÁNH ĐIỀU CHỈNH LƯU LƯỢNG		
I.S	LƯỚI CHẮN CÔN TRÙNG	NRD NRD	VAN GIÓ MỘT CHIỀU
DP	CẢM BIẾN ÁP SUẤT		
SEAG	MIỆNG HÚT	PRD PRD	VAN XẢ ÁP CƠ KHÍ

KARAOKE	BẢNG TÍNH GIẢI PHÁP BÙ KHÍ TỰ NHIÊN CHO HỆ THỐNG HÚT KHÓI			
	Tổng công suất quạt hút . Công suất quạt hút X số lượng quạt hút (m3/s)	Tổng diện tích lỗ mở bù khí trên tường ngoài . Mép trên đảm bảo khoảng cách dưới 1.5m tính từ mặt sàn, tổng 4 mặt tường (m2)	Vận tốc dòng khí vận tốc dòng khí đi qua các lỗ cửa (Yêu cầu không vượt quá 6m/s)	Kết luận khả năng bù khí tự nhiên của lỗ cửa mở
	14 3.89	1	3.2	ĐẠT YÊU CẦU

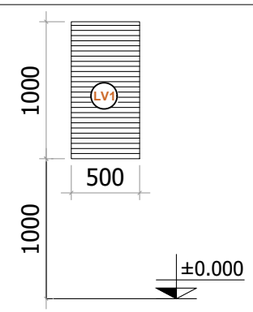

LOUVER BÙ KHÍ TỰ NHIÊN (SL : 4)
KÍCH THƯỚC 500x1000mm

MỤC ĐÍCH PHÁT HÀNH / ISSUED FOR

- ☐ THÔNG TIN / FOR INFORMATION
- ☐ DỰ TOÁN / FOR ESTIMATE
- ☑ CHẤP THUẬN / FOR APPROVAL
- ☐ ĐẤU THẦU / FOR TENDER
- ☐ ĐIỀU CHỈNH / FOR RESUBMISSION

CHỦ ĐẦU TƯ

HỘ KINH DOANH KARAOKE HOÀNG ANH

ĐƠN VỊ TƯ VẤN THIẾT KẾ

CÔNG TY TNHH MTV HOÀNG QUÂN PHÁT

Địa chỉ: 521/14 Kp. Tân Hòa, P. Đông Hòa, TP. Dĩ An, T. Bình Dương
Điện thoại: 0986 099 519 - 028 6656 6422
Email: hoangquanphat@gmail.com
website: http://pccc24.com

GIÁM ĐỐC

LÊ BÍCH TRANG

CHỦ TRÌ & THIẾT KẾ:

VŨ QUYẾT TIẾN

THỂ HIỆN:

TRẦN TRỌNG TIẾN

TÊN DỰ ÁN

CẢI TẠO KARAOKE HOÀNG ANH

Địa chỉ: KP. Bình Hòa 2, P. Tân Phước Khánh, TP. Tân Uyên, Tỉnh Bình Dương


TÊN BẢN VẼ

MẶT BẰNG HÚT KHÓI TẦNG TRỆT

HẠNG MỤC

HÚT KHÓI

KÍ HIỆU.BV	NGÀY HOÀN THÀNH
HK-02	Tháng 10/2024

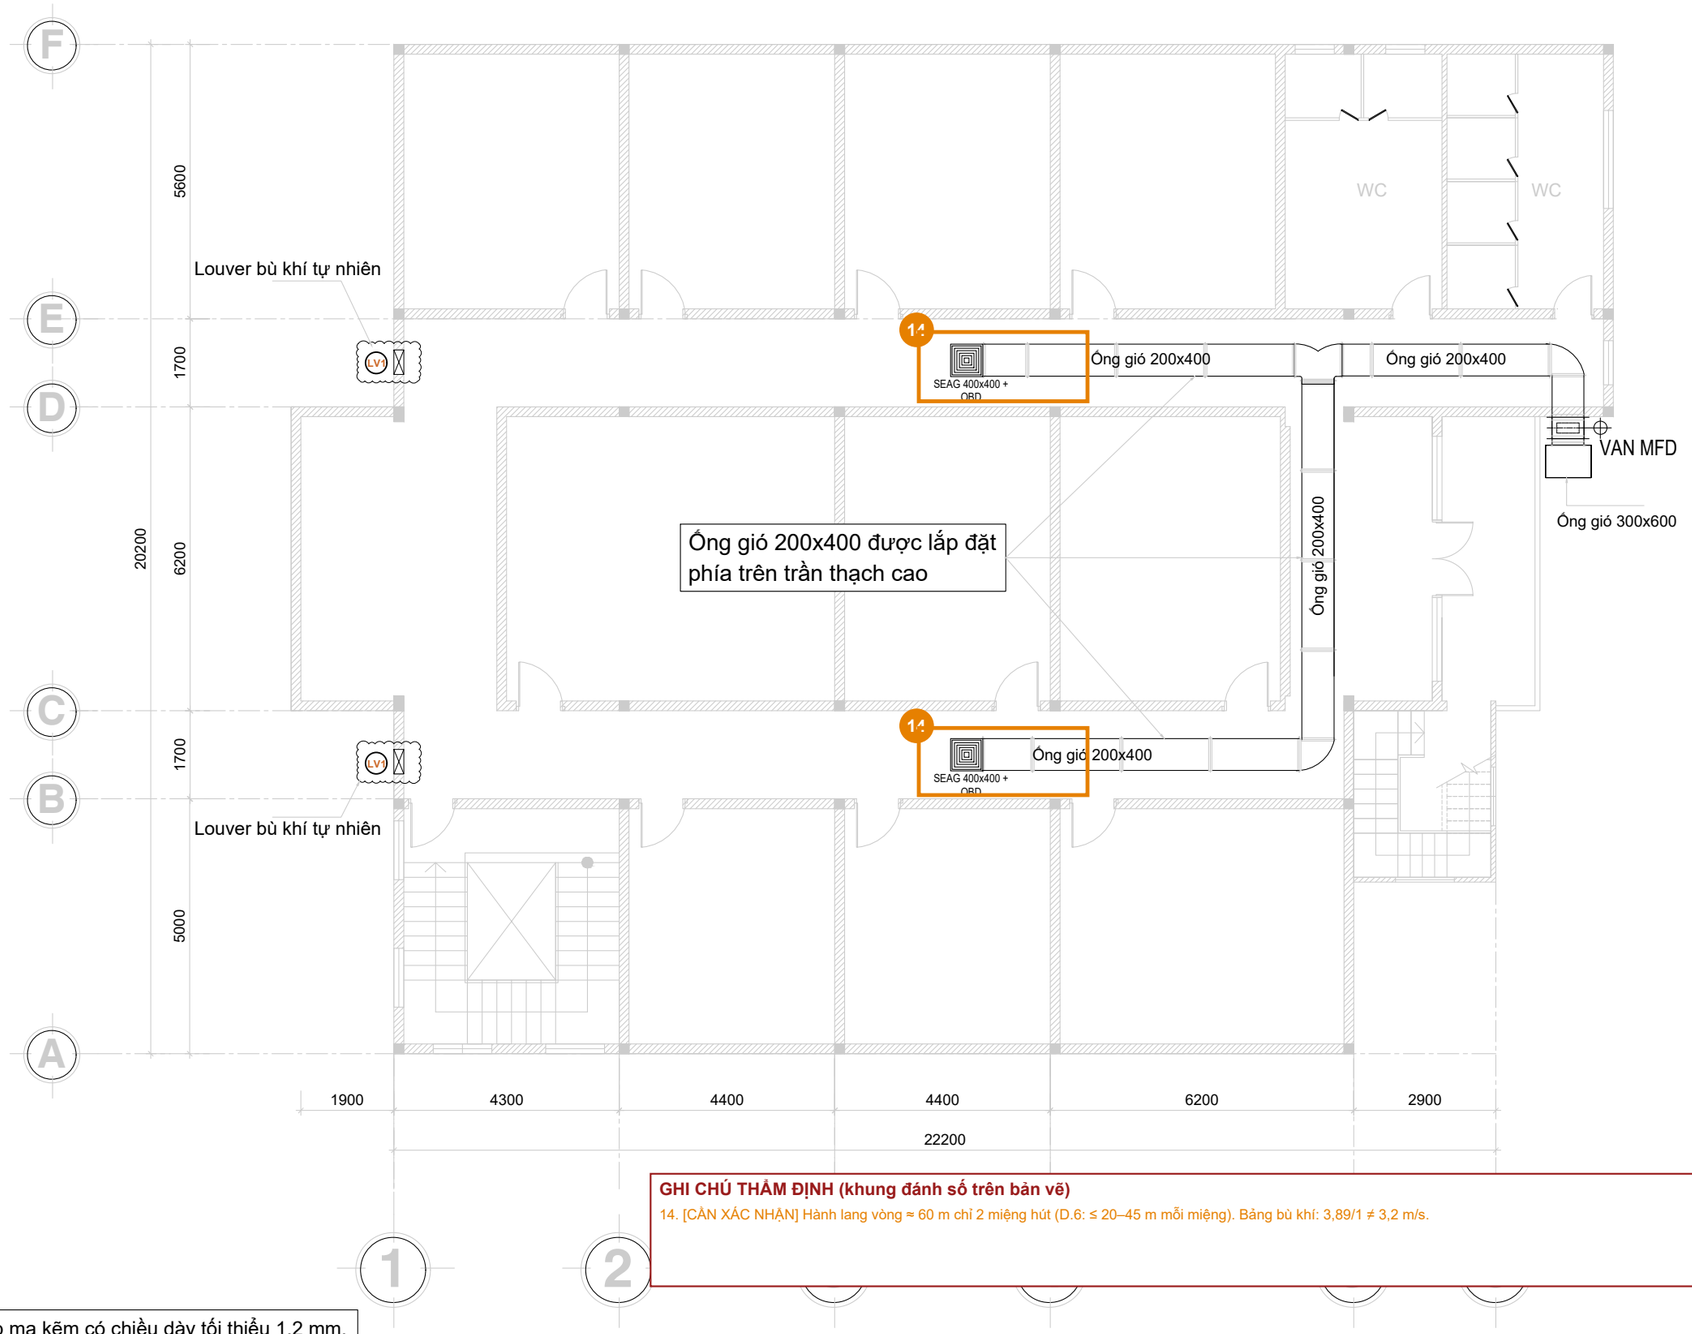

GHI CHÚ THẨM ĐỊNH (khung đánh số trên bản vẽ)


14. [CẦN XÁC NHẬN] Hành lang vòng ≈ 60 m chỉ 2 miệng hút (D.6: ≤ 20–45 m mỗi miệng). Bảng bù khí: 3,89/1 ≠ 3,2 m/s.

1) Ống gió được làm bằng thép mạ kẽm có chiều dày tối thiểu 1,2 mm.
2) toàn bộ chiều dài ống được bảo vệ bằng các đầu phun sprinkler và các đầu phun được bố trí bên trên và bên dưới ống.
3) ống và kết cấu treo, đỡ được thiết kế và thi công phù hợp với quy cách hiện hành.
=> Không yêu cầu GHCL của ống gió hút khói (chú thích 4, mục D.9 phụ lục D sửa đổi 01:2023 QCVN 06/2022-BXD).

MẶT BẰNG HÚT KHÓI LẦU 1

CHỮ VIẾT TẮT/KÝ HIỆU			
SEAG	MIỆNG HÚT KHÓI	MFD	CỬA GIÓ ĐÓNG MỞ BẰNG ĐỘNG CƠ ĐIỆN
OBD	CÁNH ĐIỀU CHỈNH LƯU LƯỢNG		
I.S	LƯỚI CHẮN CÔN TRÙNG	NRD NRD	VAN GIÓ MỘT CHIỀU
DP	CẢM BIẾN ÁP SUẤT		
SEAG	MIỆNG HÚT	PRD PRD	VAN XẢ ÁP CƠ KHÍ

KARAOKE	BẢNG TÍNH GIẢI PHÁP BÙ KHÍ TỰ NHIÊN CHO HỆ THỐNG HÚT KHÓI			
	Tổng công suất quạt hút . Công suất quạt hút X số lượng quạt hút (m3/s)	Tổng diện tích lỗ mở bù khí trên tường ngoài . Mép trên đảm bảo khoảng cách dưới 1.5m tính từ mặt sàn, tổng 4 mặt tường (m2)	Vận tốc dòng khí vận tốc dòng khí đi qua các lỗ cửa (Yêu cầu không vượt quá 6m/s)	Kết luận khả năng bù khí tự nhiên của lỗ cửa mở
	3.89	1	3.2	ĐẠT YÊU CẦU

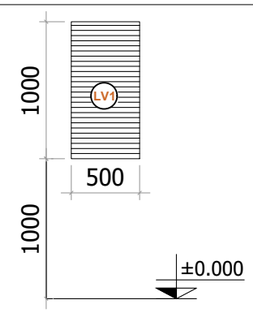

LOUVER BÙ KHÍ TỰ NHIÊN (SL : 4)
KÍCH THƯỚC 500x1000mm

MỤC ĐÍCH PHÁT HÀNH / ISSUED FOR

- ☐ THÔNG TIN / FOR INFORMATION
- ☐ DỰ TOÁN / FOR ESTIMATE
- ☑ CHẤP THUẬN / FOR APPROVAL
- ☐ ĐẤU THẦU / FOR TENDER
- ☐ ĐIỀU CHỈNH / FOR RESUBMISSION

CHỦ ĐẦU TƯ

HỘ KINH DOANH KARAOKE HOÀNG ANH

ĐƠN VỊ TƯ VẤN THIẾT KẾ

CÔNG TY TNHH MTV HOÀNG QUÂN PHÁT

Địa chỉ: 521/14 Kp. Tân Hòa, P. Đông Hòa, TP. Dĩ An, T. Bình Dương
Điện thoại: 0986 099 519 - 028 6656 6422
Email: hoangquanphat@gmail.com
website: http://pccc24.com

GIÁM ĐỐC

LÊ BÍCH TRANG

CHỦ TRÌ & THIẾT KẾ:

VŨ QUYẾT TIẾN

THỂ HIỆN:

TRẦN TRỌNG TIẾN

TÊN DỰ ÁN

CẢI TẠO KARAOKE HOÀNG ANH

Địa chỉ: KP. Bình Hòa 2, P. Tân Phước Khánh, TP. Tân Uyên, Tỉnh Bình Dương

TÊN BẢN VẼ

MẶT BẰNG HÚT KHÓI LẦU 1

HẠNG MỤC

HÚT KHÓI

KÍ HIỆU.BV	NGÀY HOÀN THÀNH
HK-03	Tháng 10/2024

TỔNG HỢP THẨM ĐỊNH – KARAOKE HOÀNG ANH 1 (kiến trúc 20-12-2024, PCCC 02-12-2024)

Bảng đối chiếu: mẫu chính thức B15 (karaoke, vũ trường). Số đo là ước lượng ±1–2 m, chưa đo trên CAD. Màu: đỏ CHƯA ĐẠT, cam CẦN XÁC NHẬN, xanh dương CHỈNH BẢN VẼ (sai sót hoặc thiếu ghi chú).

Đã xét 88 dòng của bảng B15: ĐẠT 39 · CHƯA ĐẠT 2 · CẦN XÁC NHẬN 24 · KHÔNG ÁP DỤNG 23.

1	CHƯA ĐẠT	Cửa D3 (0,8×2,1 m, GHCL '-') mở vào hành lang thoát nạn nhưng không phải cửa chống cháy. Karaoke bắt buộc ngăn cách hành lang bằng bộ phận ngăn cháy; mọi cửa mở vào hành lang phải là cửa ngăn cháy (Đ.3.3.5).
2	CHỈNH BẢN VẼ	Sửa ghi chú: 'cửa chống cháy D1 EI60' thành FD1 (D1 là cửa kính 1,9×2,3 m, GHCL '-').
3	CHỈNH BẢN VẼ	Số người lớn nhất là 105 (Lầu 1, đã xác nhận): sửa bảng thống kê và ghi chú đang ghi 93; tầng trệt 92 theo khối tính.
4	CHỈNH BẢN VẼ	Lầu 1: sửa nhãn lối thoát: lối 1 là FD1 0,9×2,1 m, lối 2 là D2 1,5×2,1 m; sửa dòng 'lối rộng 0,9 và 0,9 m' thành 0,9 và 1,5 m.
5	CHỈNH BẢN VẼ	Giới hạn ghi 40 m không khớp Bảng G.2a (bậc II, mật độ ≤ 2: 60 m giữa hai lối, 30 m hành lang cụt); sửa số. Kết luận ĐẠT không đổi.
6	CHỈNH BẢN VẼ	Ghi chú 'Sàn BTCT có GHCL REI150' mâu thuẫn thuyết minh kết cấu (sàn BTCT dày 100 mm GHCL REI45); sửa.
7	CẦN XÁC NHẬN	Hành lang trong dài hơn 15 m, không thông gió tự nhiên (Phụ lục D, D.2c): bộ PCCC đã có hút khói cơ khí, xem khung 14.
8	CẦN XÁC NHẬN	Thiếu dữ liệu: vật liệu tường và sàn hành lang. Bảng B.8 (F2.1): hành lang tường, trần CV1, sàn CV2. Chỉ ghi trần thạch cao không cháy; cần ghi thêm.
9	CHỈNH BẢN VẼ	Ghi kích thước bậc tam cấp tại D1 (đã vẽ 3 cấp) và D2 như chi tiết FD1; ghi chú D1, D2 là cửa kính hai cánh luôn đóng, đẩy thủ công mở ra, không khóa.
10	CHỈNH BẢN VẼ	Cửa FD1 cạnh P.kỹ thuật nước là cửa vào phòng kỹ thuật nằm dưới thang CT2, không phải lối thoát nạn (lối thoát nạn là lối ra ngoài). Nên ghi chú rõ 'cửa phòng kỹ thuật' và hướng mở không vào buồng thang (Đ.3.4.5). Lầu 1 cửa vào CT2 để trống không cánh, thông thủy lớn hơn 900 mm, cao hơn 1,9 m nên đạt, do người thiết kế quyết định có lắp cửa hay không.
11	CẦN XÁC NHẬN	Bảng tỉ lệ cửa/tường chỉ tính cửa FD1; tường TL3 còn có hai cửa D3 không chống cháy (Lầu 1 nằm trong đoạn 24,5 m; tầng trệt khu WC nằm ngoài đoạn 13,7 m).
12	CHỈNH BẢN VẼ	Ghi chú bề rộng chỉ tính tổng n = 105/165 = 0,64 m. Nên bổ sung kiểm tra từng lối khi một lối bị chặn (Đ.3.2.8): 105 người qua FD1 0,9 m (0,9 × 165 = 148 người, đạt). Lối vào buồng thang tính theo G.2.1.1, không áp 1,2 m.
13	CHỈNH BẢN VẼ	Mặt đứng có cao độ +7,600 nhưng chưa ghi chú 'chiều cao PCCC 7,6 m' (khoảng cách từ mặt đường xe chữa cháy đến mép dưới ô cửa tầng trên cùng, Đ.1.4.9). Bổ sung ghi chú.
14	CẦN XÁC NHẬN	Hút khói tầng trệt: hành lang khép vòng khoảng 60 m chỉ có 2 miệng hút; D.6 cho mỗi miệng ≤ 45 m (thẳng), ≤ 30 m (gấp khúc), ≤ 20 m (vòng khép kín). Bảng bù khí: 3,89 m³/s chia 1 m² là 3,89 m/s, bảng ghi 3,2 m/s.
15	CHỈNH BẢN VẼ	Thuyết minh EX–EM: E = 0,4×10 000/820 bằng 4,88 lux (ghi 12,19); diện tích ghi 1 601,7 m² nhưng tính 820 m²; khoảng cách quan sát ghi 85 m nhưng tính H với 30 m (85/200 = 0,425 m lớn hơn biển 0,202 m). Sửa số.